


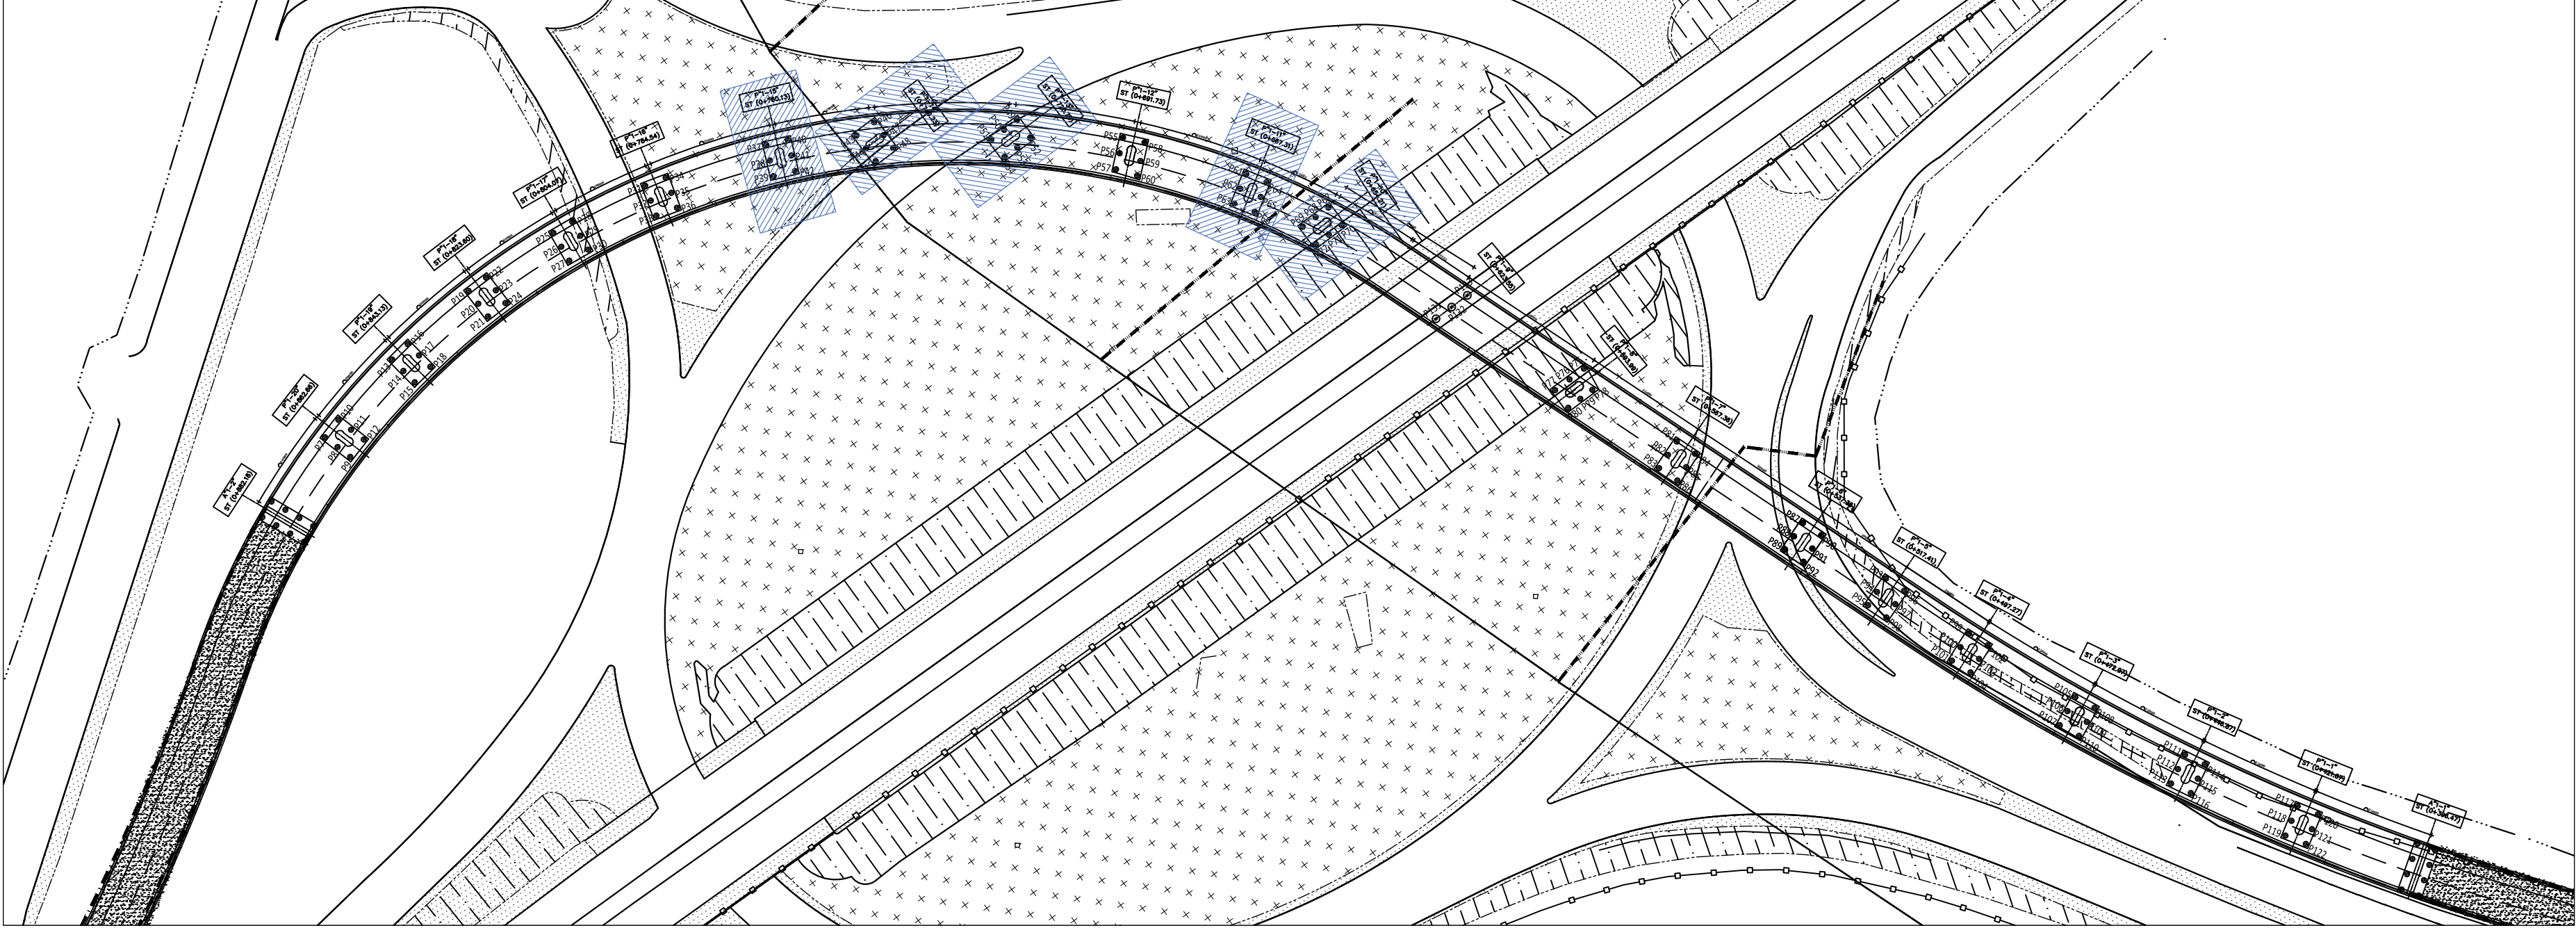

GENERAL PLAN SHOWING ARRANGEMENT OF PILES
FOR EL GHYRAN BRIDGE 01
SCALE 1: 50

.\A\$Cc40b3fd1.dib

PILECAP NAME	PILE NAME	PILE DIAMETER	PILE LENGTH	PILE EASTING	PILE NORTHING	PILE BOTTOM LEVEL	FOUNDATION BOTTOM LEVEL	CUT-OFF LEVEL
P"1-15"	37	1000 mm	28000 mm	205913.6515	3635332.6626	(-13.495)	(+14.505)	(+14.555)
	38	1000 mm	28000 mm	205912.3767	3635329.7274			
	39	1000 mm	28000 mm	205911.1020	3635326.7923			
	40	1000 mm	28000 mm	205917.6873	3635330.9098			
	41	1000 mm	28000 mm	205916.4126	3635327.9747			
	42	1000 mm	28000 mm	205915.1378	3635325.0395			
P"1-14"	43	1000 mm	28000 mm	205929.2284	3635323.3716	(-13.683)	(+14.317)	(+14.367)
	44	1000 mm	28000 mm	205929.2284	3635320.1716			
	45	1000 mm	28000 mm	205929.2284	3635316.9716			
	46	1000 mm	28000 mm	205933.6284	3635323.3716			
	47	1000 mm	28000 mm	205933.6477	3635320.1744			
	48	1000 mm	28000 mm	205933.6477	3635316.9716			
P"1-13"	49	1000 mm	28000 mm	205956.7370	3635306.6025	(-13.997)	(+14.003)	(+14.053)
	50	1000 mm	28000 mm	205953.5370	3635306.6031			
	51	1000 mm	28000 mm	205950.3370	3635306.6037			
	52	1000 mm	28000 mm	205956.7361	3635302.2031			
	53	1000 mm	28000 mm	205953.5362	3635302.2031			
	54	1000 mm	28000 mm	205950.3362	3635302.2037			
P"1-11"	61	1000 mm	28000 mm	205987.0213	3635270.5510	(-13.536)	(+14.464)	(+14.514)
	62	1000 mm	28000 mm	205984.2898	3635268.8839			
	63	1000 mm	28000 mm	205981.5584	3635267.2169			
	64	1000 mm	28000 mm	205989.3135	3635266.7952			
	65	1000 mm	28000 mm	205986.5820	3635265.1282			
	66	1000 mm	28000 mm	205983.8505	3635263.4611			
P"1-10"	67	1000 mm	28000 mm	205996.1599	3635255.3329	(-13.744)	(+14.256)	(+14.306)
	68	1000 mm	28000 mm	205992.9599	3635255.3329			
	69	1000 mm	28000 mm	205989.7599	3635255.3329			
	70	1000 mm	28000 mm	205996.1599	3635250.9329			
	71	1000 mm	28000 mm	205992.9599	3635250.9329			
	72	1000 mm	28000 mm	205989.7599	3635250.9329			

- NOTES:-
1. ALL DIMENSIONS ARE IN MILLIMETERS UNLESS OTHERWISE SPECIFIED.
 2. ALL DIMENSIONS AND LEVELS MUST BE CHECKED WITH THE PLANNING DRAWINGS.
 3. DO NOT MEASURE FROM DRAWINGS. ALL DIMENSION SHOULD BE READ OR COMPUTED.
 4. COMPRESSIVE STRENGTH OF REINFORCED CONCRETE SHALL BE NOT LESS THAN THESE VALUES :
 - PILES C25/30
 - PRECASTED BEAMS C35/45
 - REMAINING ELEMENTS C30/37
 5. MINIMUM CONCRETE COVER FOR REINFORCEMENT UNLESS OTHERWISE INDICATED ON DRAWINGS SHALL BE AS FOLLOWS:
 - PILES 60 mm
 - PRECASTED BEAMS 30 mm
 - REMAINING ELEMENTS 40 mm
 6. STEEL USED OF GRADE 400 MPA.



REINFORCEMENT NOTATION :
01 20 Y 25 - @ 100
↑ SPACING IN (mm.)
↑ NOMINAL DIAMETER OF BAR IN (mm.)
↑ HIGH YIELD STEEL GRADE
↑ QUANTITY NOS OF BARS
↑ BAR MARK

ABBREVIATIONS:			
P	PILE	STAGG.	STAGGERED
AX.	AXIS	S.B.	SIDE BAR
N.T.S.	NOT TO SCALE	ST.	STARTER BAR
B	BOTTOM		
T	TOP		
ADD.	ADDITIONAL		
O.S.	OUTER STIRRUP		
I.S.	INNER STIRRUP		

DESIGN DRAWINGS REFS :	
TTPP-GNR-GH1-WES-EDDW-00005-00008	
TTPP-GNR-GH1-WES-EDDW-00011-00016	
TTPP-GNR-GH1-WES-EDDW-00028	

SPECIFICATIONS REFS :	
GEG-ENG-SPC-0000-TRR-005-04	

01	P(1-12) EXCLUDED	O.G	29-04-2026
00	ISSUED FOR INFORMATION	A.A	09-02-2026
REV.	DESCRIPTION	DRAWN BY	DATE

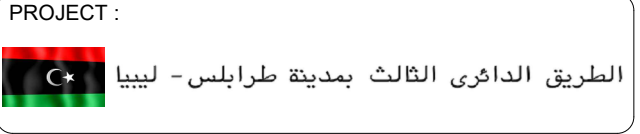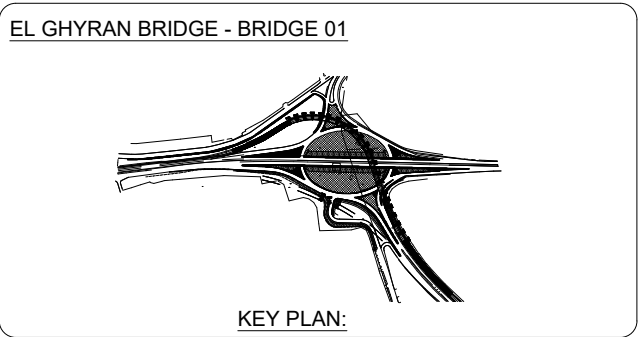

SHOP DRAWING TITLE :			
EL GHYRAN // EL GHYRAN BRIDGE 01 TYPICAL PILE REINFORCEMENT DETAILS FOR AXIS ((P"1-10"~P"1-11")&(P"1-13"~P"1-15")) (2/2)			
Dwg.No:	TTRR-GHY-GHY1-OHRNJV-CDF-05-EDWG-00011		
REVISION	01	DRAWN	A.A
SCALE	AS SHOWN	REVIEWED	A.E.
DATE	FEB.-2026	APPROVED	K.N.