


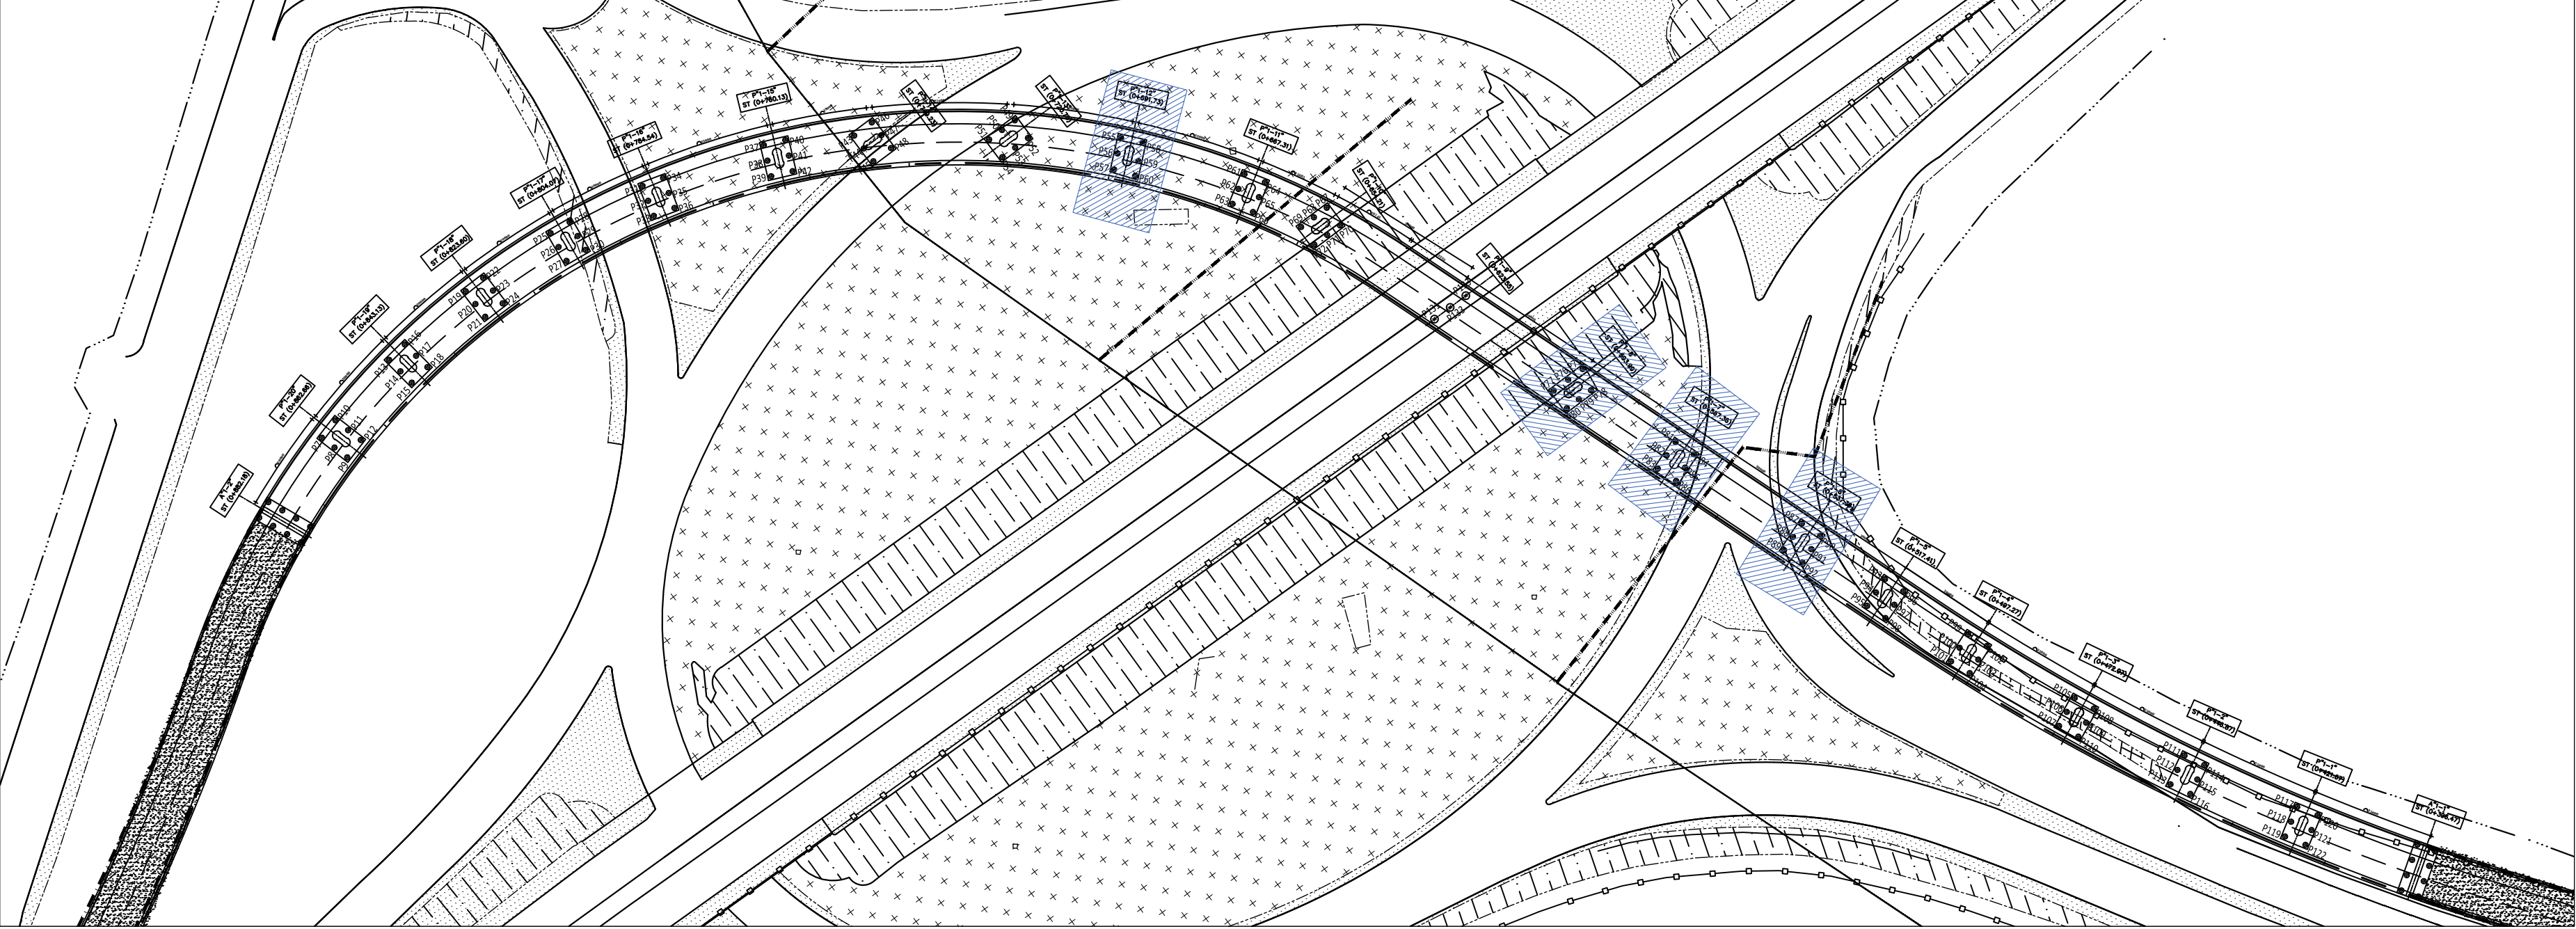

GENERAL PLAN SHOWING ARRANGEMENT OF PILES
FOR EL GHYRAN BRIDGE 01
SCALE 1: 50

PILECAP NAME	PILE NAME	PILEDIAMETER	PILELENGTH	PILEEASTING	PILENORTHING	PILEBOTTOM LEVEL	FOUNDATION BOTTOM LEVEL	CUT-OFF LEVEL
P"1-8"	75	1000 mm	30000 mm	206010.5700	3635198.9593	(-15.088)	(+14.912)	(+14.962)
	76	1000 mm	30000 mm	206014.1700	3635198.9593			
	77	1000 mm	30000 mm	206017.7700	3635198.9593			
	78	1000 mm	30000 mm	206016.5700	3635194.5593			
	79	1000 mm	30000 mm	206013.5700	3635194.5593			
	80	1000 mm	30000 mm	206010.5700	3635194.5593			
P"1-7"	81	1000 mm	30000 mm	206023.9111	3635176.1558	(-16.285)	(+13.715)	(+13.765)
	82	1000 mm	30000 mm	206020.8929	3635175.0927			
	83	1000 mm	30000 mm	206017.8746	3635174.0295			
	84	1000 mm	30000 mm	206025.3729	3635172.0058			
	85	1000 mm	30000 mm	206022.3547	3635170.9426			
	86	1000 mm	30000 mm	206019.3365	3635169.8794			
P"1-6"	87	1000 mm	30000 mm	206034.3497	3635148.0265	(-16.465)	(+13.535)	(+13.585)
	88	1000 mm	30000 mm	206031.3315	3635146.9633			
	89	1000 mm	30000 mm	206028.3133	3635145.9001			
	90	1000 mm	30000 mm	206035.8116	3635143.8764			
	91	1000 mm	30000 mm	206032.7934	3635142.8132			
	92	1000 mm	30000 mm	206029.7751	3635141.7501			
P"1-12"	55	1000 mm	30000 mm	205966.7249	3635286.8830	(-15.669)	(+14.331)	(+14.381)
	56	1000 mm	30000 mm	205969.2138	3635289.0193			
	57	1000 mm	30000 mm	205971.6420	3635291.1035			
	58	1000 mm	30000 mm	205974.5078	3635287.7648			
	59	1000 mm	30000 mm	205971.6243	3635285.2898			
	60	1000 mm	30000 mm	205969.3479	3635283.3359			

3 - 4 - 1769 ط د

TTRR-GE-CHIB2-EPC1-OHRNJV-HI-TRN-3185-02
TTRR-GE-CHIB2-EPC1-OHRNJV-HI-TRN-3210-020

.\A\$Cc40b3fd1.dib

NOTES:-

1. ALL DIMENSIONS ARE IN MILLIMETERS UNLESS OTHERWISE SPECIFIED.
2. ALL DIMENSIONS AND LEVELS MUST BE CHECKED WITH THE PLANNING DRAWINGS.
3. DO NOT MEASURE FROM DRAWINGS. ALL DIMENSION SHOULD BE READ OR COMPUTED.
4. COMPRESSIVE STRENGTH OF REINFORCED CONCRETE SHALL BE NOT LESS THAN THESE VALUES :
 - PILES _____ C25/30
 - PRECASTED BEAMS _____ C35/45
 - REMAINING ELEMENTS _____ C30/37
5. MINIMUM CONCRETE COVER FOR REINFORCEMENT UNLESS OTHERWISE INDICATED ON DRAWINGS SHALL BE AS FOLLOWS:
 - PILES _____ 60 mm
 - PRECASTED BEAMS _____ 30 mm
 - REMAINING ELEMENTS _____ 40 mm
6. STEEL USED OF GRADE 400 MPA.

REINFORCEMENT NOTATION :

01 20 Y 25 - @ 100
↑ ↑ ↑ ↑ ↑
BAR MARK QUANTITY NOS OF BARS HIGH YIELD STEEL GRADE NOMINAL DIAMETER OF BAR IN (mm.) SPACING IN (mm.)

ABBREVIATIONS:

P	PILE	STAGG.	STAGGERED
AX.	AXIS	S.B.	SIDE BAR
N.T.S.	NOT TO SCALE	ST.	STARTER BAR
B	BOTTOM		
T	TOP		
ADD.	ADDITIONAL		
O.S.	OUTER STIRRUP		
I.S.	INNER STIRRUP		

DESIGN DRAWINGS REFS :


TTPP-GNR-GH1-WES-EDDW-00005-00008	3 - 4 - 1769 ط د
TTPP-GNR-GH1-WES-EDDW-00011-00016	
TTPP-GNR-GH1-WES-EDDW-00029-C	
TTRR-GE-CHIB2-EPC1-OHRNJV-HI-TRN-3185-01	

SPECIFICATIONS REFS :

GEG-ENG-SPC-0000-TRR-005-04	

02	ISSUED FOR INFORMATION	O.G	29-04-2026
01	ISSUED FOR INFORMATION	A.A	09-02-2026
00	ISSUED FOR INFORMATION	A.A	09-02-2026
REV.	DESCRIPTION	DRAWN BY	DATE

EL GHYRAN BRIDGE - BRIDGE 01

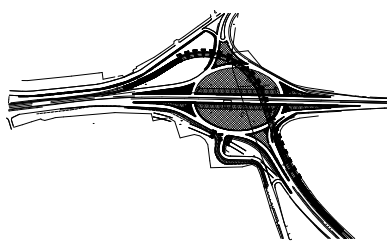

KEY PLAN:

OWNER :




OWNER'S CONSULTANT :



CONTRACTOR:



PROJECT :

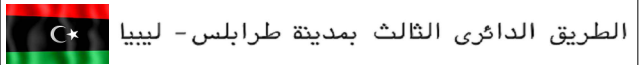

SHOP DRAWING TITLE :

EL GHYRAN // EL GHYRAN BRIDGE 01
TYPICAL PILE REINFORCEMENT DETAILS
FOR AXIS ((P"1-6"~P"1-8") & (P"1-12")

(2/2)

Dwg.No:	TTRR-GHY-GHY1-OHRNJV-CDF-05-EDWG-00008		
REVISION	02	DRAWN	O.G
SCALE	AS SHOWN	REVIEWED	K.N
DATE	FEB.-2026	APPROVED	K.N.