


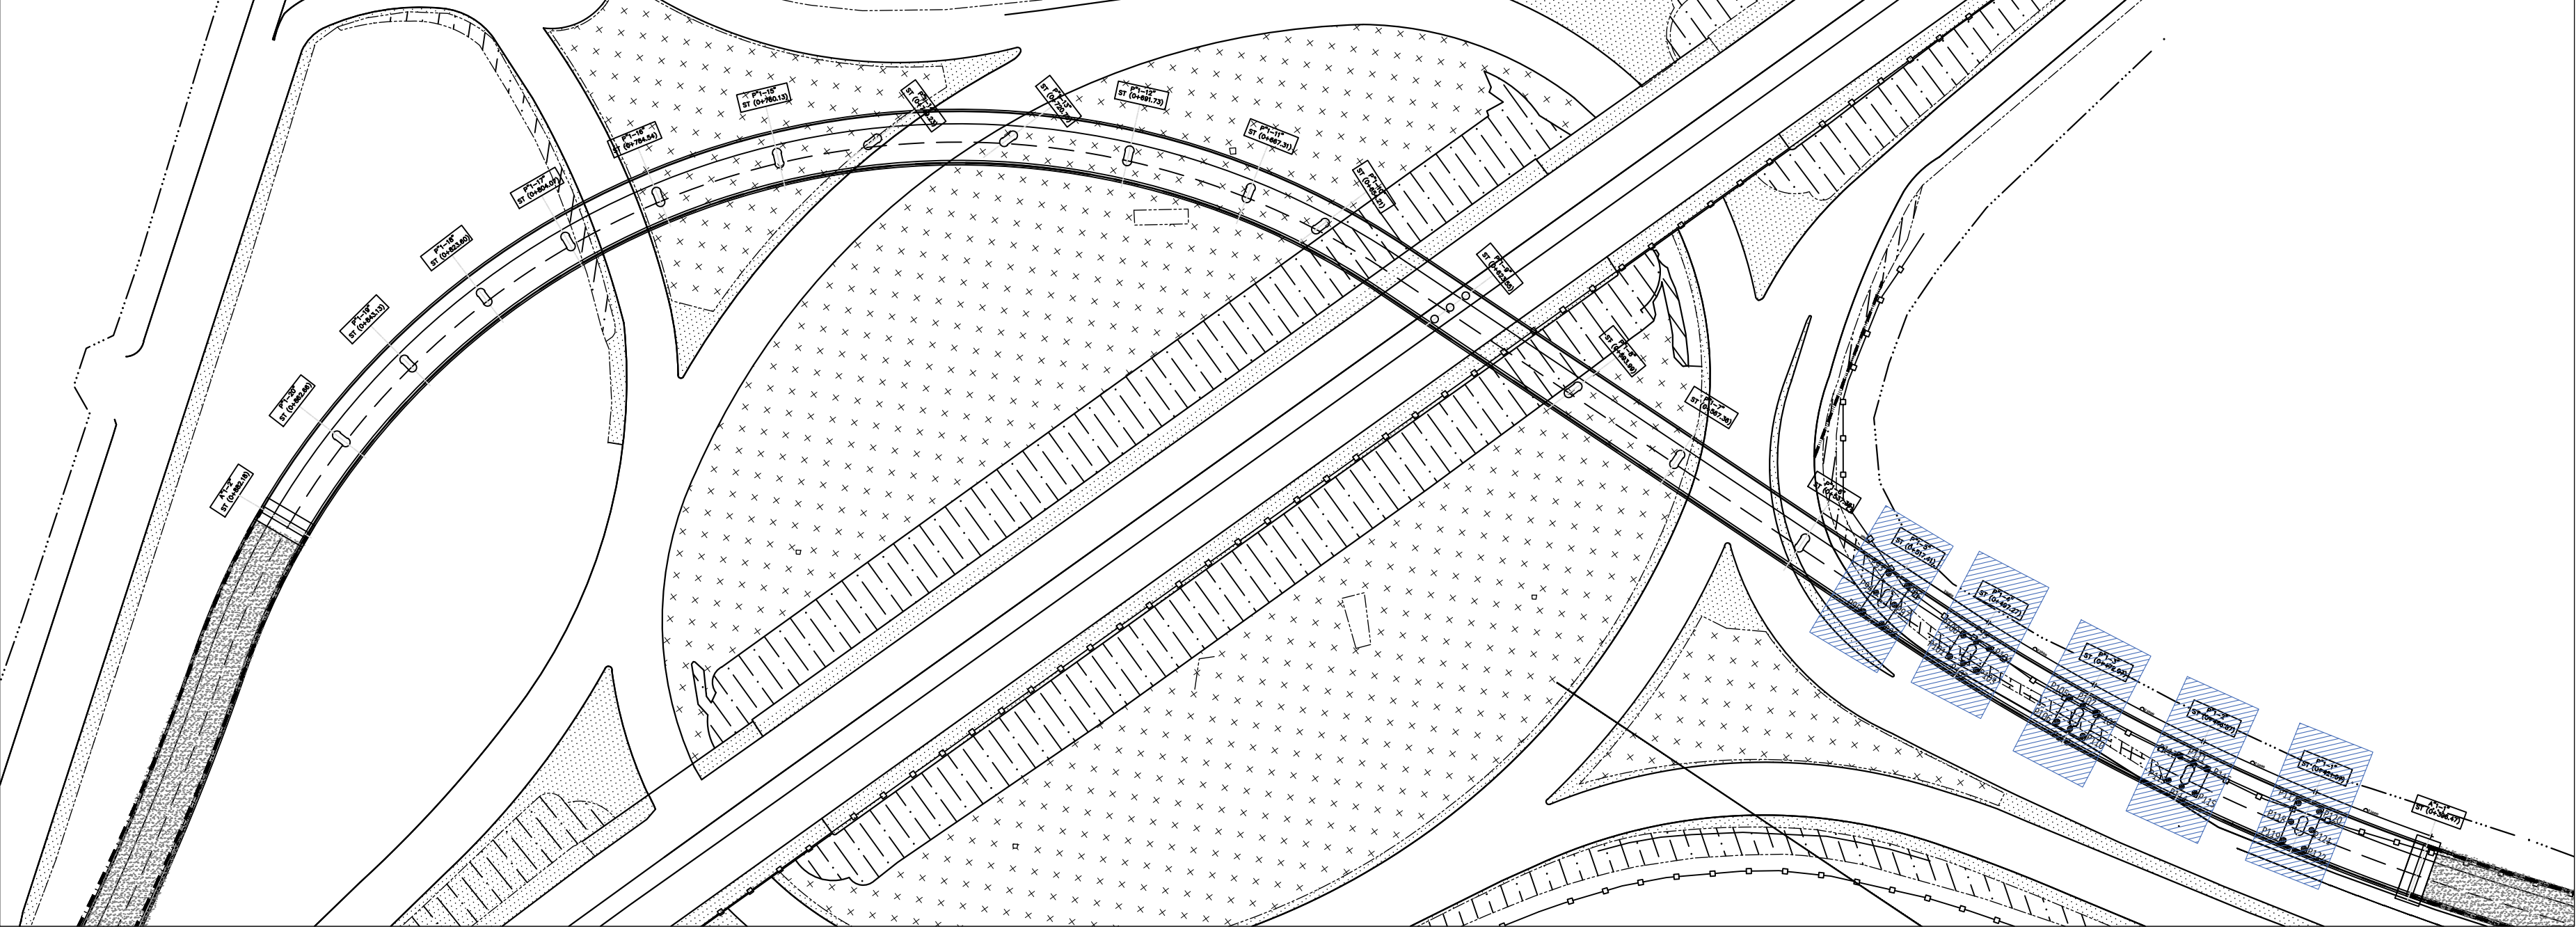

GENERAL PLAN SHOWING ARRANGEMENT OF PILES  
FOR EL GHYRAN BRIDGE 01  
SCALE 1: 50

| PILECAP NAME | PILE NAME | PILE DIAMETER | PILE LENGTH | PILE EASTING | PILE NORTHING | PILE BOTTOM LEVEL | FOUNDATION BOTTOM LEVEL | CUT-OFF LEVEL |
|--------------|-----------|---------------|-------------|--------------|---------------|-------------------|-------------------------|---------------|
| P"1-5"       | 93        | 1000 mm       | 25000 mm    | 206042.2521  | 3635129.6557  | (-11.177)         | (+13.823)               | (+13.873)     |
|              | 94        | 1000 mm       | 25000 mm    | 206037.9606  | 3635128.1440  |                   |                         |               |
|              | 95        | 1000 mm       | 25000 mm    | 206033.6690  | 3635126.6323  |                   |                         |               |
|              | 96        | 1000 mm       | 25000 mm    | 206043.7139  | 3635125.5056  |                   |                         |               |
|              | 97        | 1000 mm       | 25000 mm    | 206039.4224  | 3635123.9940  |                   |                         |               |
|              | 98        | 1000 mm       | 25000 mm    | 206035.1309  | 3635122.4823  |                   |                         |               |
| P"1-4"       | 99        | 1000 mm       | 25000 mm    | 206048.0144  | 3635108.2135  | (-10.872)         | (+14.128)               | (+14.178)     |
|              | 100       | 1000 mm       | 25000 mm    | 206046.7638  | 3635110.8300  |                   |                         |               |
|              | 101       | 1000 mm       | 25000 mm    | 206042.1890  | 3635109.0746  |                   |                         |               |
|              | 102       | 1000 mm       | 25000 mm    | 206043.4397  | 3635106.4581  |                   |                         |               |
|              | 103       | 1000 mm       | 25000 mm    | 206044.6903  | 3635103.8416  |                   |                         |               |
|              | 104       | 1000 mm       | 25000 mm    | 206049.2651  | 3635105.5971  |                   |                         |               |
| P"1-3"       | 105       | 1000 mm       | 25000 mm    | 206056.2918  | 3635087.9517  | (-10.181)         | (+14.819)               | (+14.869)     |
|              | 106       | 1000 mm       | 25000 mm    | 206051.4856  | 3635085.7909  |                   |                         |               |
|              | 107       | 1000 mm       | 25000 mm    | 206057.4810  | 3635085.3067  |                   |                         |               |
|              | 108       | 1000 mm       | 25000 mm    | 206052.6748  | 3635083.1459  |                   |                         |               |
|              | 109       | 1000 mm       | 25000 mm    | 206058.6701  | 3635082.6617  |                   |                         |               |
|              | 110       | 1000 mm       | 25000 mm    | 206053.8639  | 3635080.5009  |                   |                         |               |
| P"1-2"       | 111       | 1000 mm       | 25000 mm    | 206068.2819  | 3635062.9962  | (-9.42)           | (+15.58)                | (+15.63)      |
|              | 112       | 1000 mm       | 25000 mm    | 206066.9462  | 3635065.5704  |                   |                         |               |
|              | 113       | 1000 mm       | 25000 mm    | 206062.2684  | 3635063.1433  |                   |                         |               |
|              | 114       | 1000 mm       | 25000 mm    | 206063.6040  | 3635060.5691  |                   |                         |               |
|              | 115       | 1000 mm       | 25000 mm    | 206064.9396  | 3635057.9950  |                   |                         |               |
|              | 116       | 1000 mm       | 25000 mm    | 206069.6174  | 3635060.4222  |                   |                         |               |
| P"1-1"       | 117       | 1000 mm       | 25000 mm    | 206080.3422  | 3635043.9250  | (-8.697)          | (+16.303)               | (+16.353)     |
|              | 118       | 1000 mm       | 25000 mm    | 206076.9120  | 3635041.8674  |                   |                         |               |
|              | 119       | 1000 mm       | 25000 mm    | 206073.4818  | 3635039.8098  |                   |                         |               |
|              | 120       | 1000 mm       | 25000 mm    | 206082.6051  | 3635040.1515  |                   |                         |               |
|              | 121       | 1000 mm       | 25000 mm    | 206079.1749  | 3635038.0939  |                   |                         |               |
|              | 122       | 1000 mm       | 25000 mm    | 206075.7447  | 3635036.0363  |                   |                         |               |

- NOTES:-
1. ALL DIMENSIONS ARE IN MILLIMETERS UNLESS OTHERWISE SPECIFIED.
  2. ALL DIMENSIONS AND LEVELS MUST BE CHECKED WITH THE PLANNING DRAWINGS.
  3. DO NOT MEASURE FROM DRAWINGS. ALL DIMENSION SHOULD BE READ OR COMPUTED.
  4. COMPRESSIVE STRENGTH OF REINFORCED CONCRETE SHALL BE NOT LESS THAN THESE VALUES :
    - PILES \_\_\_\_\_ C25/30
    - PRECASTED BEAMS \_\_\_\_\_ C35/45
    - REMAINING ELEMENTS \_\_\_\_\_ C30/37
  5. MINIMUM CONCRETE COVER FOR REINFORCEMENT UNLESS OTHERWISE INDICATED ON DRAWINGS SHALL BE AS FOLLOWS:
    - PILES \_\_\_\_\_ 60 mm
    - PRECASTED BEAMS \_\_\_\_\_ 30 mm
    - REMAINING ELEMENTS \_\_\_\_\_ 40 mm
  6. STEEL USED OF GRADE 400 MPA.

REINFORCEMENT NOTATION :

01 20 Y 25 - @ 100

SPACING IN (mm.)

NOMINAL DIAMETER OF BAR IN (mm.)

HIGH YIELD STEEL GRADE

QUANTITY NOS OF BARS

BAR MARK

ABBREVIATIONS:

|        |               |        |             |
|--------|---------------|--------|-------------|
| P      | PILE          | STAGG. | STAGGERED   |
| AX.    | AXIS          | S.B.   | SIDE BAR    |
| N.T.S. | NOT TO SCALE  | ST.    | STARTER BAR |
| B      | BOTTOM        |        |             |
| T      | TOP           |        |             |
| ADD.   | ADDITIONAL    |        |             |
| O.S.   | OUTER STIRRUP |        |             |
| I.S.   | INNER STIRRUP |        |             |



DESIGN DRAWINGS REFS :

|                                          |  |
|------------------------------------------|--|
| TTPP-GNR-GH1-WES-EDDW-00005-00008        |  |
| TTPP-GNR-GH1-WES-EDDW-00011-00016        |  |
| TTPP-GNR-GH1-WES-EDDW-00018              |  |
| TTRR-GE-CHIB2-EPC1-OHRNJV-HI-TRN-3239-02 |  |

SPECIFICATIONS REFS :

|                              |  |
|------------------------------|--|
| GEG-ENG-SPC-0000-TRR-005-004 |  |
|                              |  |
|                              |  |

|      |                        |          |            |
|------|------------------------|----------|------------|
| 03   | ISSUED FOR INFORMATION | O.G      | 09-06-2026 |
| 02   | ISSUED FOR INFORMATION | O.G      | 23-05-2026 |
| 01   | ISSUED FOR INFORMATION | A.A      | 01-01-2026 |
| 00   | ISSUED FOR INFORMATION | A.A      | 20-12-2025 |
| REV. | DESCRIPTION            | DRAWN BY | DATE       |

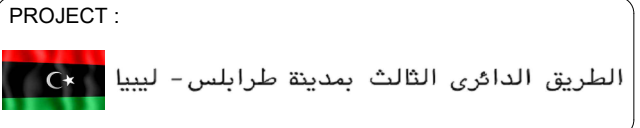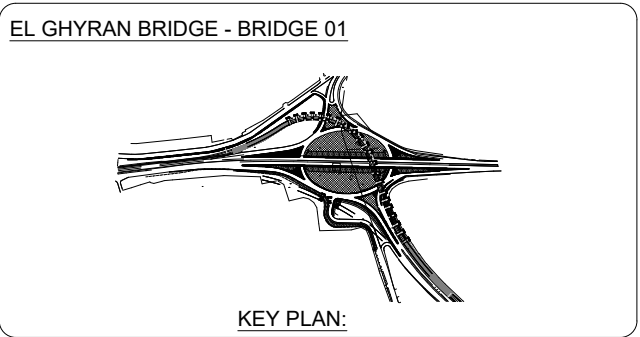

SHOP DRAWING TITLE :

EL GHYRAN // EL GHYRAN BRIDGE 01  
TYPICAL PILE REINFORCEMENT DETAILS  
FOR AXIS ((P"1-1" TO P"1-5") (2/2)

|          |                                        |          |      |
|----------|----------------------------------------|----------|------|
| Dwg.No:  | TTRR-GHY-GHY1-OHRNJV-CDF-05-EDWG-00002 |          |      |
| REVISION | 03                                     | DRAWN    | A.A  |
| SCALE    | AS SHOWN                               | REVIEWED | A.E. |
| DATE     | JAN.-2026                              | APPROVED | K.N. |