


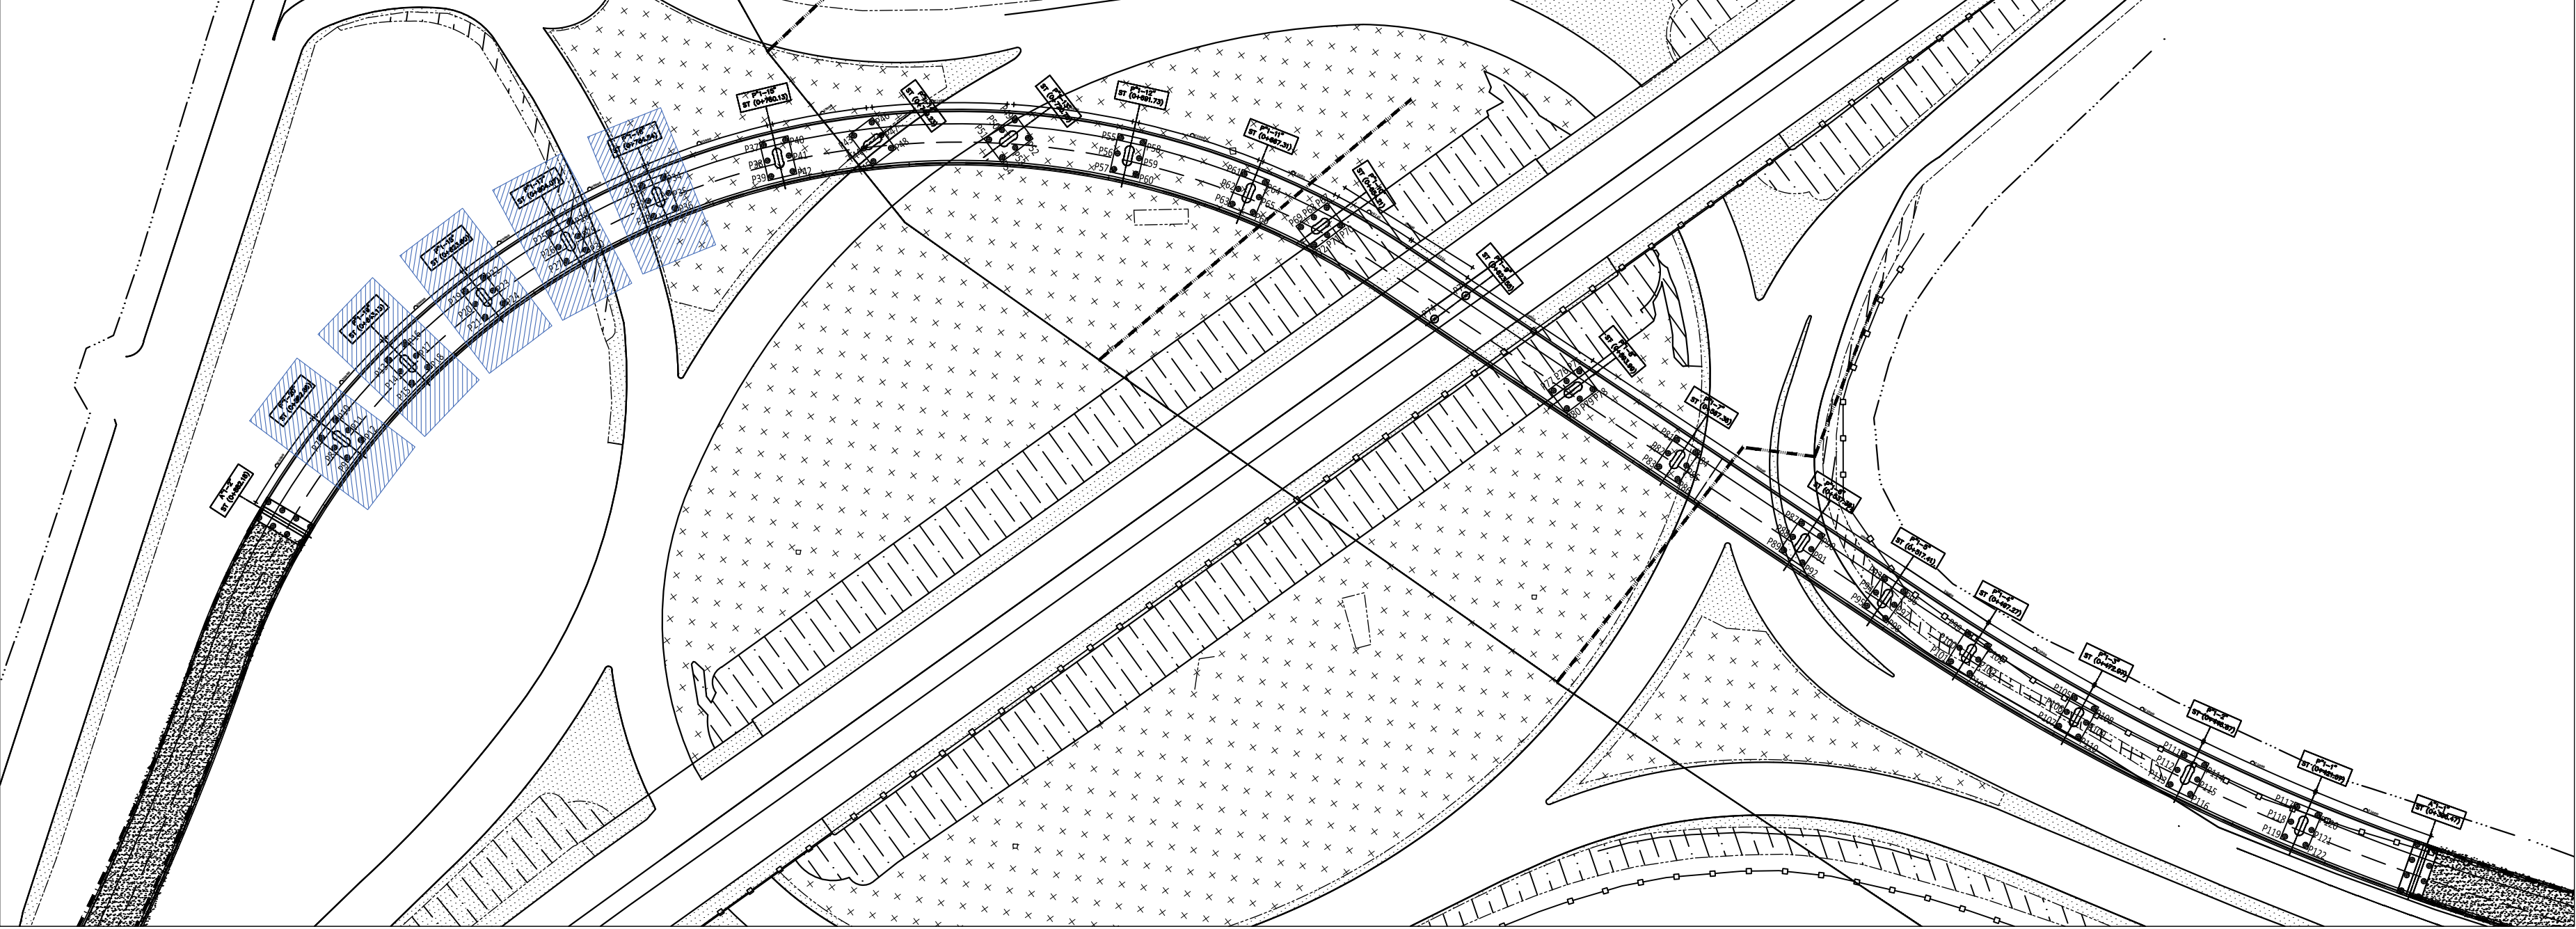

GENERAL PLAN SHOWING ARRANGEMENT OF PILES
FOR EL GHYRAN BRIDGE 01
SCALE 1: 50

- NOTES:-
1. ALL DIMENSIONS ARE IN MILLIMETERS UNLESS OTHERWISE SPECIFIED.
 2. ALL DIMENSIONS AND LEVELS MUST BE CHECKED WITH THE PLANNING DRAWINGS.
 3. DO NOT MEASURE FROM DRAWINGS. ALL DIMENSION SHOULD BE READ OR COMPUTED.
 4. COMPRESSIVE STRENGTH OF REINFORCED CONCRETE SHALL BE NOT LESS THAN THESE VALUES :
 - PILES C25/30
 - PRECASTED BEAMS C35/45
 - REMAINING ELEMENTS C30/37
 5. MINIMUM CONCRETE COVER FOR REINFORCEMENT UNLESS OTHERWISE INDICATED ON DRAWINGS SHALL BE AS FOLLOWS:
 - PILES 60 mm
 - PRECASTED BEAMS 30 mm
 - REMAINING ELEMENTS 40 mm
 6. STEEL USED OF GRADE 400 MPA.

REINFORCEMENT NOTATION :

01 20 Y 25 - @ 100

SPACING IN (mm.)

NOMINAL DIAMETER OF BAR IN (mm.)

HIGH YIELD STEEL GRADE

QUANTITY NOS OF BARS

BAR MARK

ABBREVIATIONS:			
P	PILE	STAGG.	STAGGERED
AX.	AXIS	S.B.	SIDE BAR
N.T.S.	NOT TO SCALE	ST.	STARTER BAR
B	BOTTOM		
T	TOP		
ADD.	ADDITIONAL		
O.S.	OUTER STIRRUP		
I.S.	INNER STIRRUP		

DESIGN DRAWINGS REFS :	
TTPP-GNR-GH1-WES-EDDW-00005-00008	
TTPP-GNR-GH1-WES-EDDW-00011-00016	
TTPP-GNR-GH1-WES-EDDW-00025	
TTRR-GE-CHIB2-EPC1-OHRNVJ-HI-TRN-3007-04	

SPECIFICATIONS REFS :	
GEG-ENG-SPC-0000-TRR-005-04	

01	ISSUED FOR INFORMATION	A.A.	28-01-2026
00	ISSUED FOR INFORMATION	A.A.	04-01-2026
REV.	DESCRIPTION	DRAWN BY	DATE

EL GHYRAN BRIDGE - BRIDGE 01

KEY PLAN:

OWNER :

Housing and infrastructure board

OWNER'S CONSULTANT :

Hill International

CONTRACTOR:

EETILAF

PROJECT :

الطريق الدائري الثالث بمدينة طرابلس - ليبيا

SHOP DRAWING TITLE :

EL GHYRAN // EL GHYRAN BRIDGE 01
TYPICAL PILE REINFORCEMENT DETAILS
FOR AXIS ((P"1-16"-P"1-20") (2/2)

Dwg.No:	TTRR-GHY-GHY1-OHRNVJ-CDF-05-EDWG-00004		
REVISION	01	DRAWN	A.A
SCALE	AS SHOWN	REVIEWED	A.E.
DATE	JAN.-2026	APPROVED	K.N.

PILECAP NAME	PILE NAME	PILE DIAMETER	PILE LENGTH	PILE EASTING	PILE NORTHING	PILE BOTTOM LEVEL	FOUNDATION BOTTOM LEVEL	CUT-OFF LEVEL
P"1-20"	7	1000 mm	24000 mm	205808.0185	3635338.7259	(-7.971)	(+16.029)	(+16.129)
	8	1000 mm	24000 mm	205808.8660	3635335.6401			
	9	1000 mm	24000 mm	205809.7136	3635332.5544			
	10	1000 mm	24000 mm	205812.2614	3635339.8912			
	11	1000 mm	24000 mm	205813.1089	3635336.8055			
	12	1000 mm	24000 mm	205813.9565	3635333.7198			
P"1-19"	13	1000 mm	24000 mm	205828.0711	3635343.1162	(-8.166)	(+15.834)	(+15.934)
	14	1000 mm	24000 mm	205828.5147	3635339.9471			
	15	1000 mm	24000 mm	205828.9583	3635336.7780			
	16	1000 mm	24000 mm	205832.4287	3635343.7262			
	17	1000 mm	24000 mm	205832.8722	3635340.5570			
	18	1000 mm	24000 mm	205833.3158	3635337.3879			
P"1-18"	19	1000 mm	24000 mm	205848.5191	3635344.9308	(-8.108)	(+15.892)	(+15.992)
	20	1000 mm	24000 mm	205848.5504	3635341.7407			
	21	1000 mm	24000 mm	205848.5816	3635338.5311			
	22	1000 mm	24000 mm	205852.9189	3635344.9835			
	23	1000 mm	24000 mm	205852.9501	3635341.7837			
	24	1000 mm	24000 mm	205852.9814	3635338.5839			
P"1-17"	25	1000 mm	24000 mm	205869.0330	3635344.0937	(-9.67)	(+14.33)	(+14.43)
	26	1000 mm	24000 mm	205868.6515	3635340.9165			
	27	1000 mm	24000 mm	205868.2700	3635337.7393			
	28	1000 mm	24000 mm	205873.4016	3635343.5691			
	29	1000 mm	24000 mm	205873.0201	3635340.3919			
	30	1000 mm	24000 mm	205872.6386	3635337.2148			
P"1-16"	31	1000 mm	24000 mm	205889.3840	3635340.6579	(-9.276)	(+14.724)	(+14.824)
	32	1000 mm	24000 mm	205888.4977	3635337.5831			
	33	1000 mm	24000 mm	205887.6113	3635334.5083			
	34	1000 mm	24000 mm	205893.6119	3635339.4391			
	35	1000 mm	24000 mm	205892.7255	3635336.3643			
	36	1000 mm	24000 mm	205891.8392	3635333.2895			