
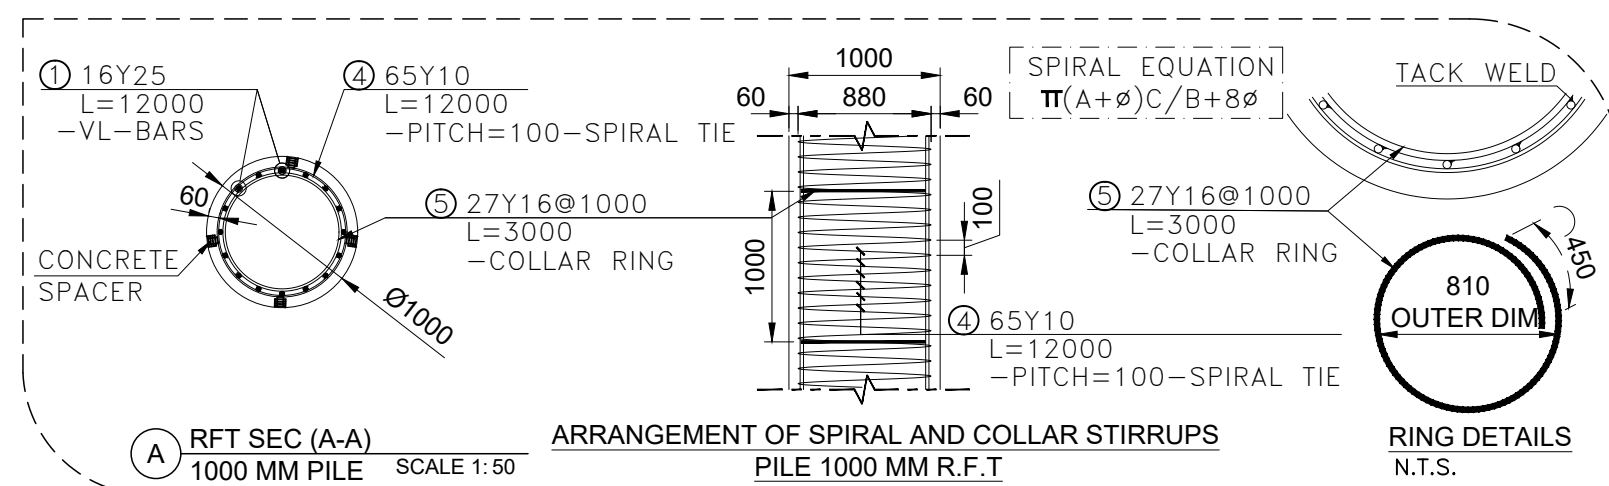
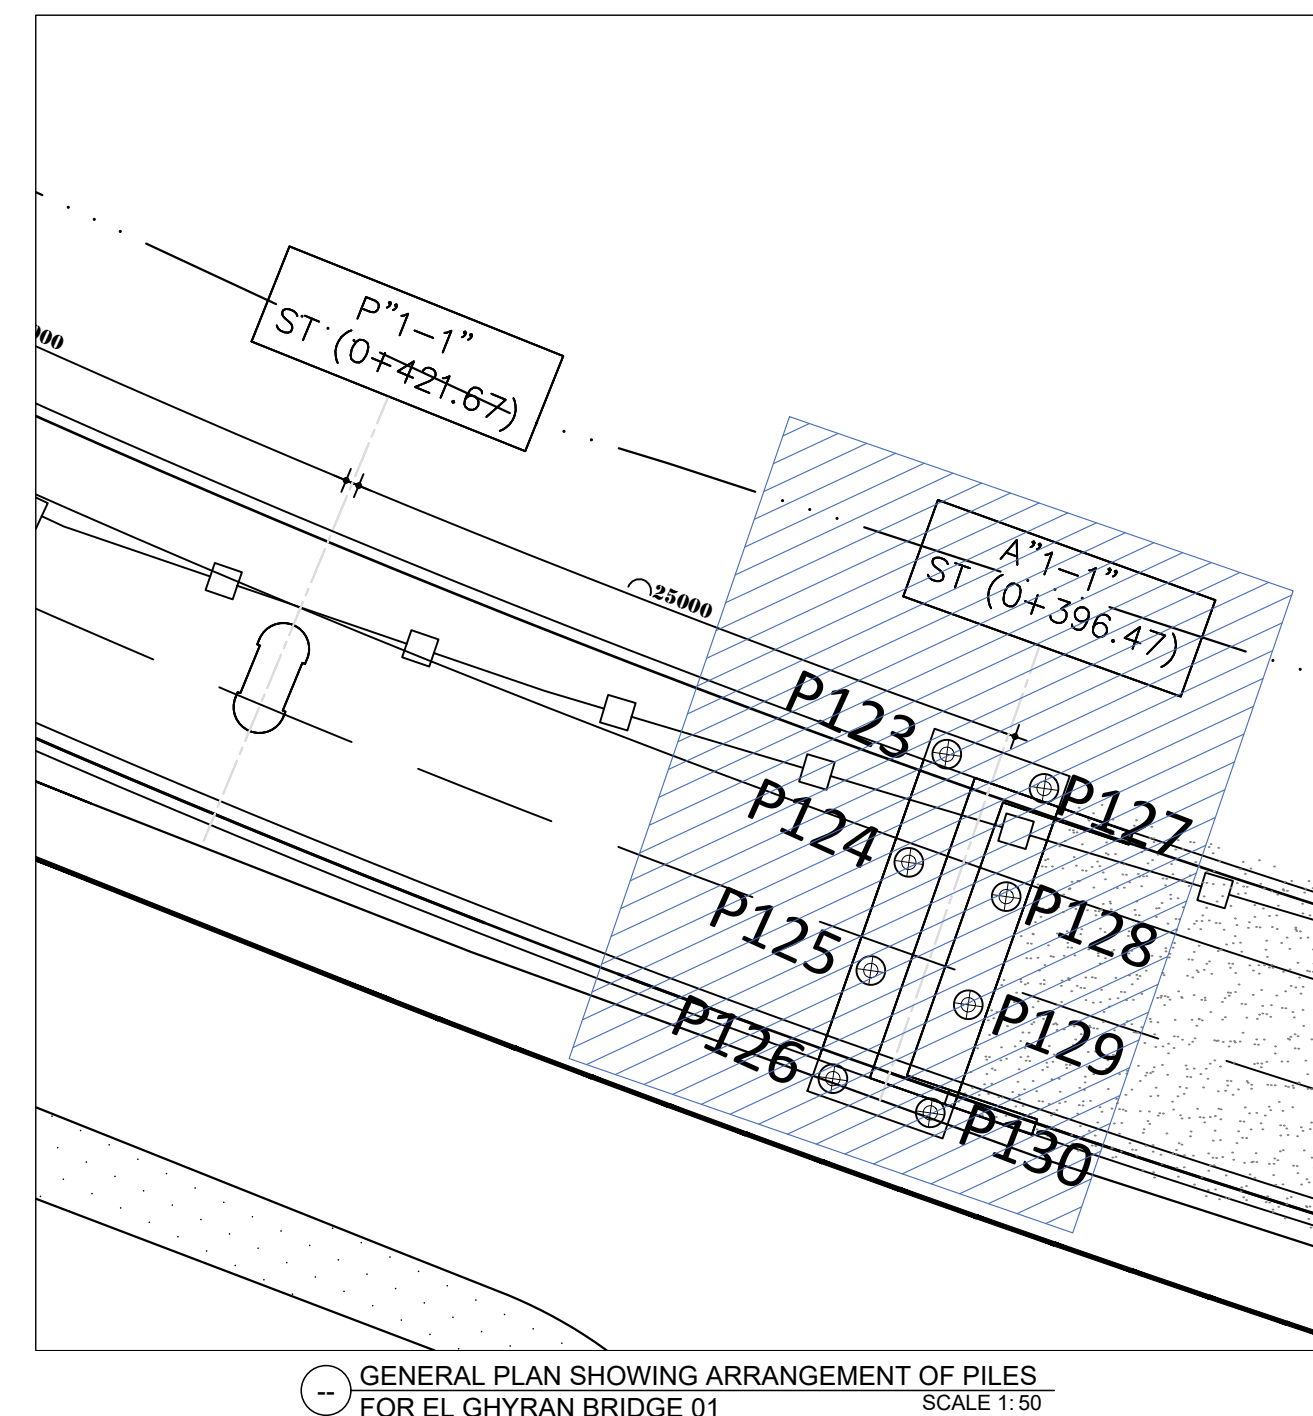


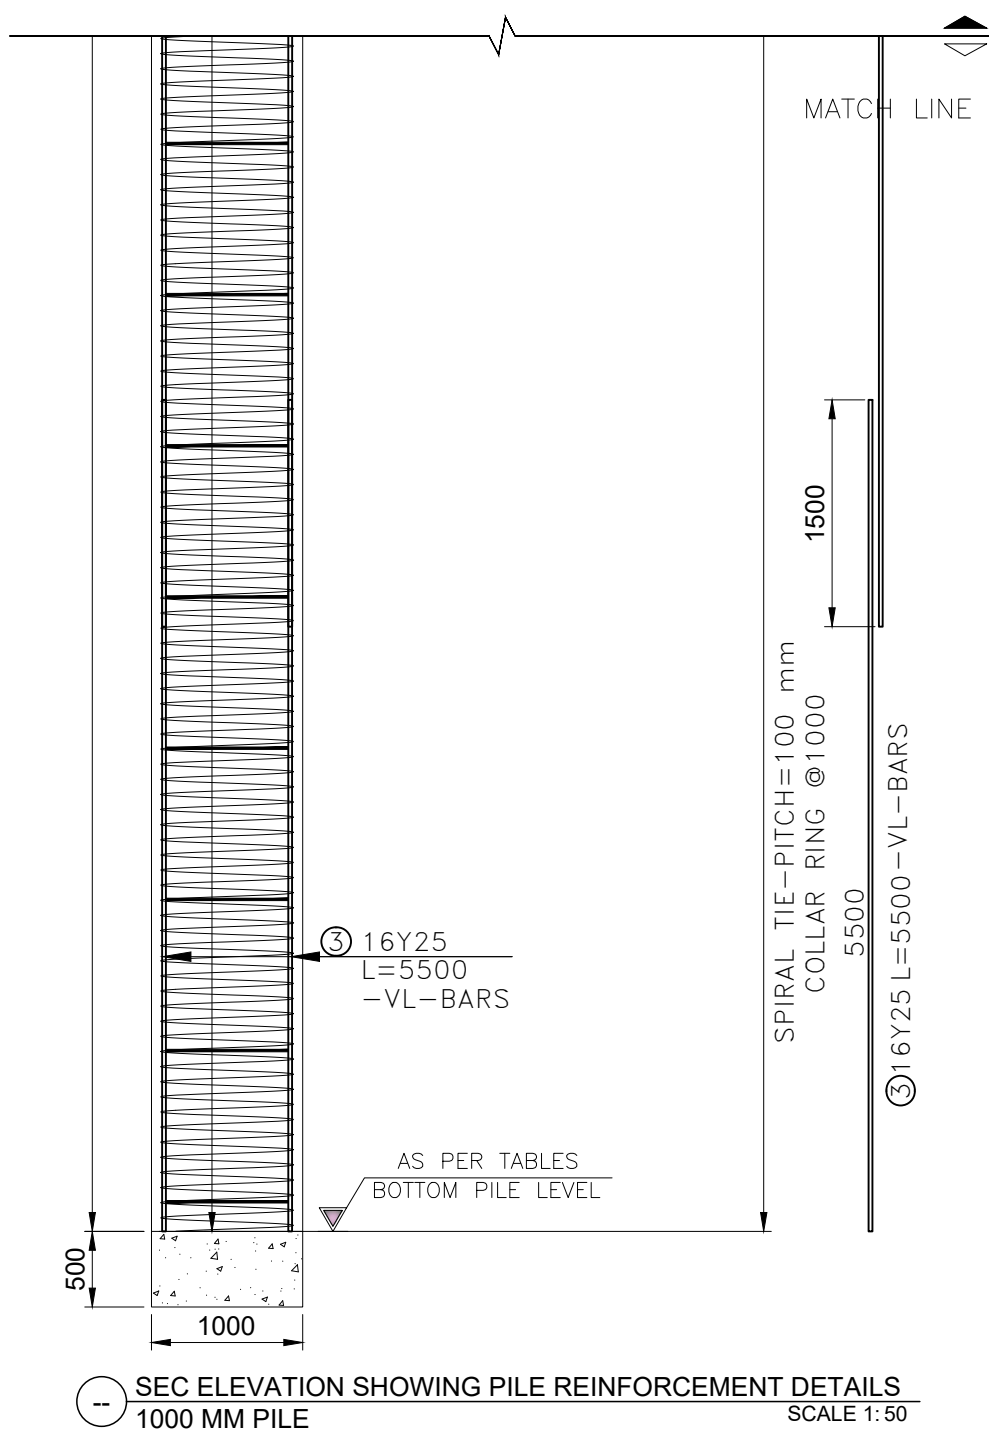


PILECAP NAME	PILE NAME	PILEDIAMETER	PILELENGTH	PILEEASTING	PILENORTHING	PILEBOTTOM LEVEL	FOUNDATION BOTTOM LEVEL	CUT-OFF LEVEL
A"1-1"	123	1000 mm	25000 mm	206095.3252	3635023.731	(-8.053)	(+16.947)	(+16.997)
	124	1000 mm	25000 mm	206092.0033	3635021.502			
	125	1000 mm	25000 mm	206088.6815	3635019.274			
	126	1000 mm	25000 mm	206085.3596	3635017.046			
	127	1000 mm	25000 mm	206097.3307	3635020.741			
	128	1000 mm	25000 mm	206094.0101	3635018.511			
	129	1000 mm	25000 mm	206090.6882	3635016.283			
	130	1000 mm	25000 mm	206087.3664	3635014.054			

MATERIAL TABLE			
CONCRETE:	EN1992-1-1	EN206-1	MINIMUM COVER
PILES	C25/30	XC2	6cm
PRE CASTED BEAMS:	C35/45	XC4	3cm
REMAINING ELEMENTS	C30/37	XC4	4cm
STEEL:			
REINFORCEMENT STEEL	EN10080-S400C (fyk = 400 MPa - EN 1992-1-1)		
PRESTRESS STEEL	EN10138-3-Y-1860S7-15,7 (S=1,50 cm² - fyd = 1426 MPa)		

- NOTES:-**
1. ALL DIMENSIONS ARE IN MILLIMETERS UNLESS OTHERWISE SPECIFIED.
 2. ALL DIMENSIONS AND LEVELS MUST BE CHECKED WITH THE PLANNING DRAWINGS.
 3. DO NOT MEASURE FROM DRAWINGS. ALL DIMENSION SHOULD BE READ OR COMPUTED.
 4. COMPRESSIVE STRENGTH OF REINFORCED CONCRETE SHALL BE NOT LESS THAN THESE VALUES :
 - PILES _____ C25/30
 - PRECASTED BEAMS _____ C35/45
 - REMAINING ELEMENTS _____ C30/37
 5. MINIMUM CONCRETE COVER FOR REINFORCEMENT UNLESS OTHERWISE INDICATED ON DRAWINGS SHALL BE AS FOLLOWS:
 - PILES _____ 60 mm
 - PRECASTED BEAMS _____ 30 mm
 - REMAINING ELEMENTS _____ 40 mm
 6. STEEL USED OF GRADE 400 MPA.

REINFORCEMENT NOTATION :

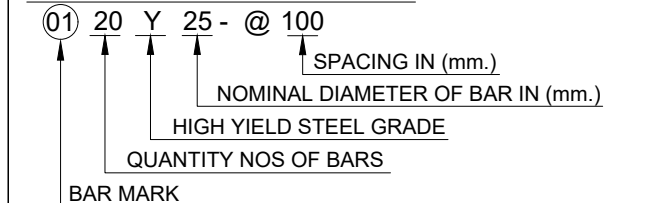

ABBREVIATIONS:

P	PILE	STAGG.	STAGGERED
AX.	AXIS	S.B.	SIDE BAR
N.T.S.	NOT TO SCALE	ST.	STARTER BAR
B	BOTTOM		
T	TOP		
ADD.	ADDITIONAL		
O.S.	OUTER STIRRUP		
I.S.	INNER STIRRUP		

DESIGN DRAWINGS REFS :


TTPP-GNR-GH1-WES-EDDW-00005-00008	
TTPP-GNR-GH1-WES-EDDW-00011-00016	
TTPP-GNR-GH1-WES-EDDW-00019	
TTRR-GE-CHIB2-EPC1-OHRNJV-HI-TRN-3239-00	

SPECIFICATIONS REFS :

GEG-ENG-SPC-0000-TRR-005-04	

00	ISSUED FOR INFORMATION	O.G	23-05-2026
00	ISSUED FOR INFORMATION	A.A	20-01-2026
REV.	DESCRIPTION	DRAWN BY	DATE

EL GHYRAN BRIDGE - BRIDGE 01

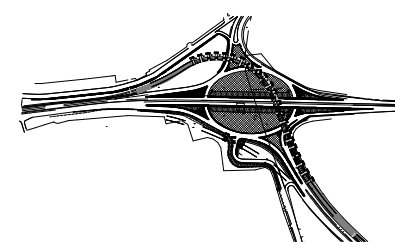

KEY PLAN:

OWNER :




OWNER'S CONSULTANT :



CONTRACTOR:



PROJECT :

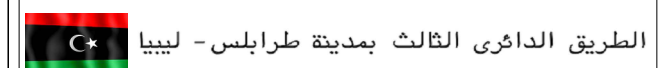

SHOP DRAWING TITLE :

EL GHYRAN // EL GHYRAN BRIDGE 01
TYPICAL PILE REINFORCEMENT DETAILS
FOR AXIS (A"1-1") (1/1)

Dwg.No:	TTRR-GHY-GHY1-OHRNJV-CDF-05-EDWG-00005		
REVISION	01	DRAWN	A.A
SCALE	AS SHOWN	REVIEWED	A.E.
DATE	JAN.-2026	APPROVED	K.N.