
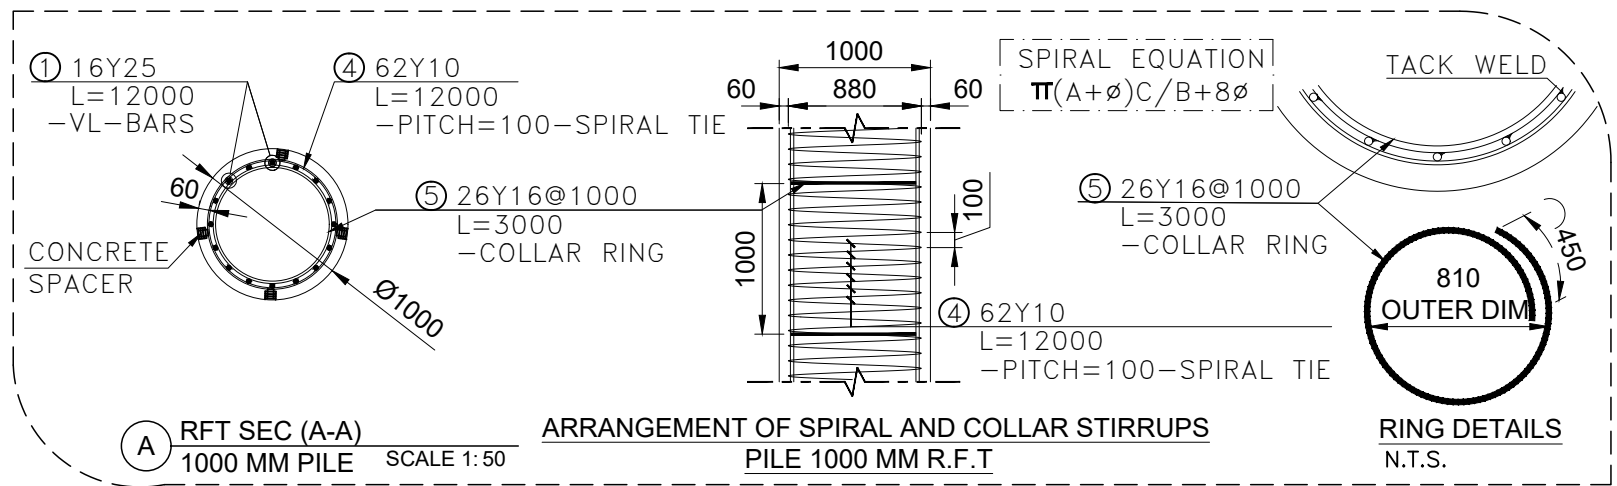
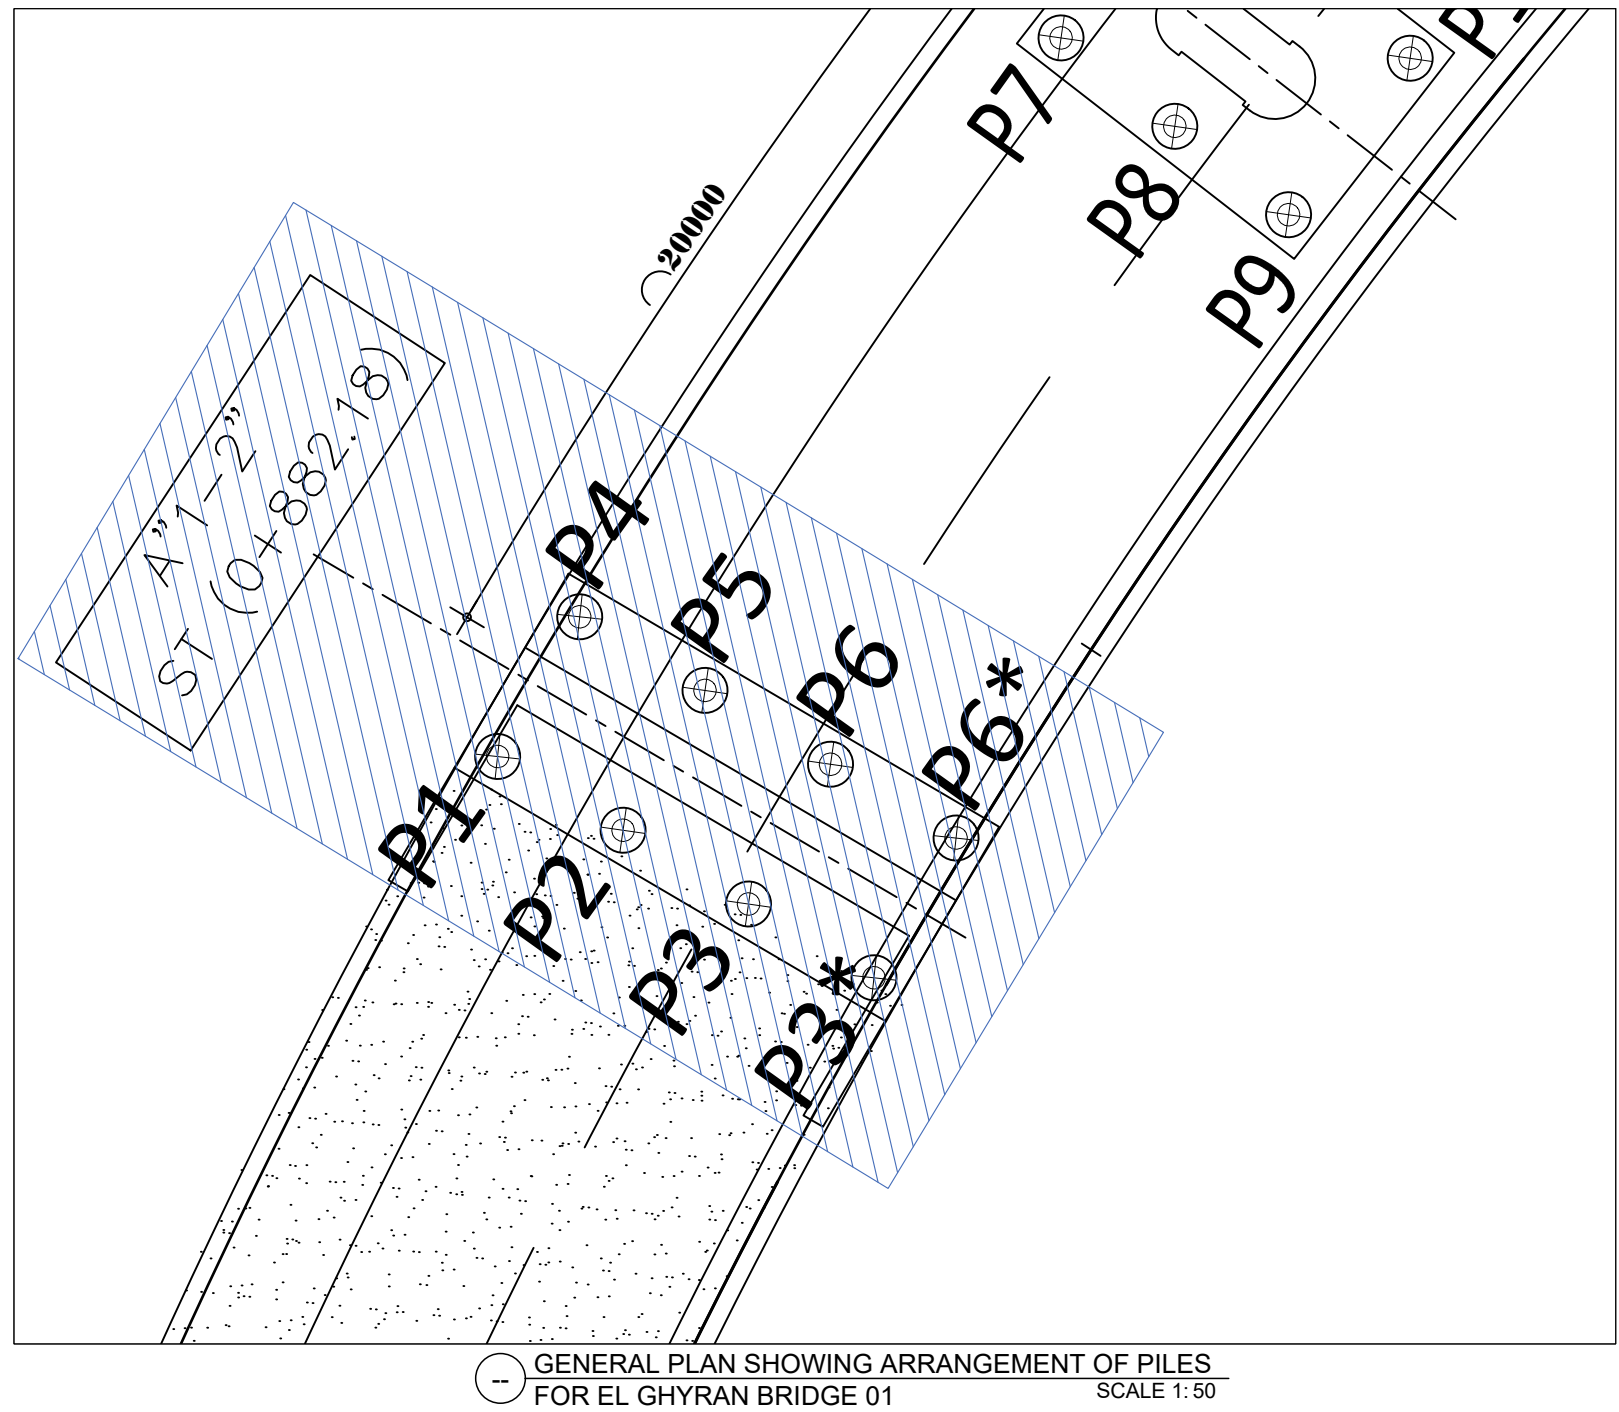


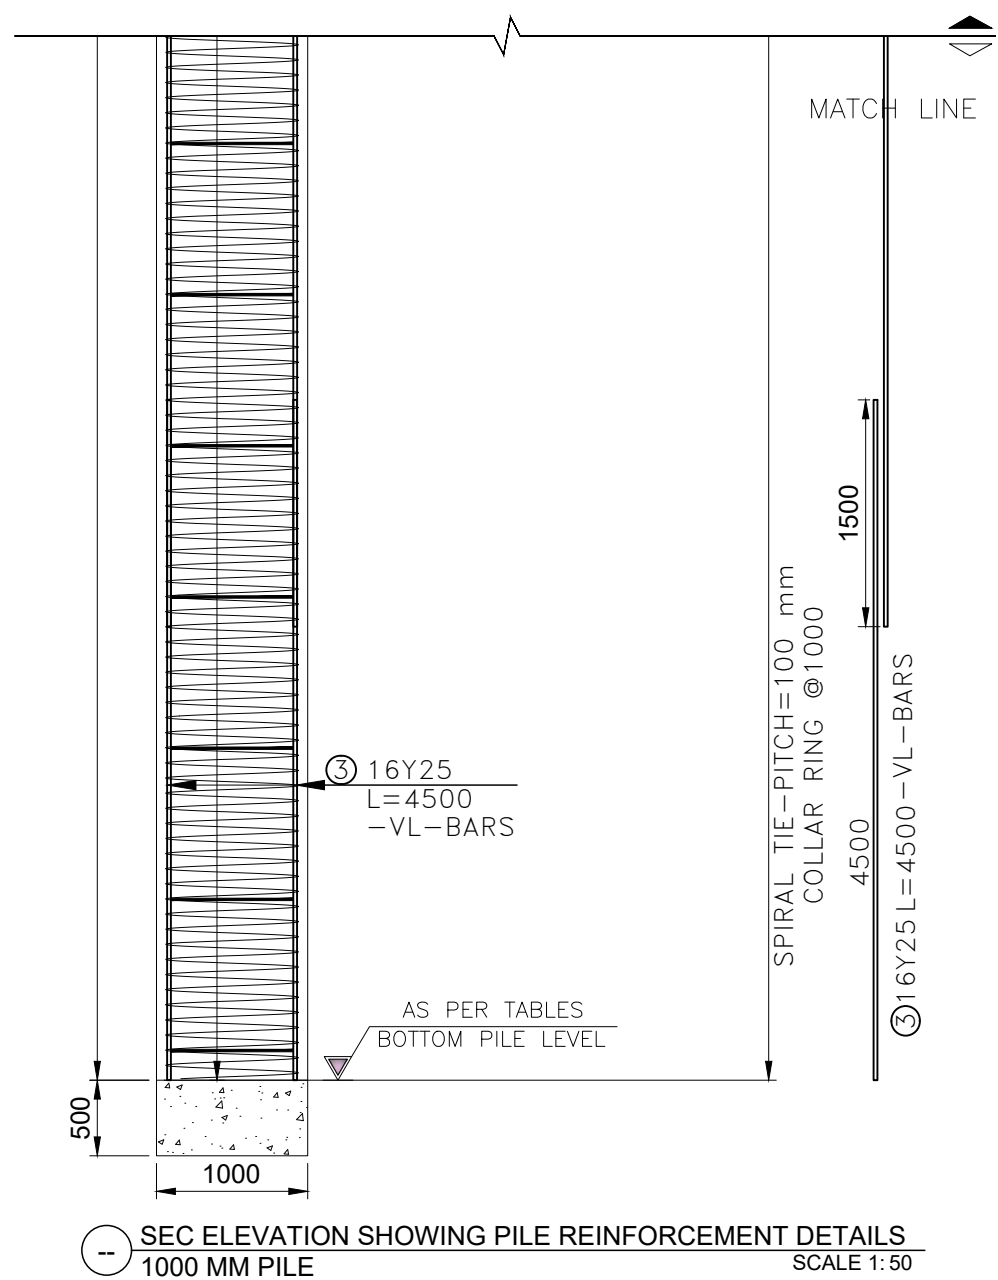


PILE CAP NAME	PILE NAME	PILE DIAMETER	PILE LENGTH	PILE EASTING	PILE NORTHING	PILE BOTTOM LEVEL	FOUNDATION BOTTOM LEVEL	CUT-OFF LEVEL
A"1-2"	P1	1000 mm	24000 mm	205788.4361	3635333.4410	(-7.979)	(+16.021)	(+16.121)
	P2	1000 mm	24000 mm	205789.6861	3635330.4599			
	P3	1000 mm	24000 mm	205790.9361	3635327.4789			
	P3*	1000 mm	24000 mm	205792.1861	3635324.4978			
	P4	1000 mm	24000 mm	205791.7557	3635334.8340			
	P5	1000 mm	24000 mm	205793.0042	3635331.8564			
	P6	1000 mm	24000 mm	205794.2549	3635328.8736			
	P6*	1000 mm	24000 mm	205795.5057	3635325.8908			

MATERIAL TABLE			
CONCRETE:	EN1992-1-1	EN206-1	MINIMUM COVER
PILES	C25/30	XC2	6cm
PRE CASTED BEAMS:	C35/45	XC4	3cm
REMAINING ELEMENTS	C30/37	XC4	4cm
STEEL:			
REINFORCEMENT STEEL	EN10080-S400C (fyk = 400 MPa - EN 1992-1-1)		
PRESTRESS STEEL	EN10138-3-Y-1860S7-15,7 (S=1,50 cm² - fyd = 1426 MPa)		

- NOTES:-**
1. ALL DIMENSIONS ARE IN MILLIMETERS UNLESS OTHERWISE SPECIFIED.
 2. ALL DIMENSIONS AND LEVELS MUST BE CHECKED WITH THE PLANNING DRAWINGS.
 3. DO NOT MEASURE FROM DRAWINGS. ALL DIMENSION SHOULD BE READ OR COMPUTED.
 4. COMPRESSIVE STRENGTH OF REINFORCED CONCRETE SHALL BE NOT LESS THAN THESE VALUES :
 - PILES _____ C25/30
 - PRECASTED BEAMS _____ C35/45
 - REMAINING ELEMENTS _____ C30/37
 5. MINIMUM CONCRETE COVER FOR REINFORCEMENT UNLESS OTHERWISE INDICATED ON DRAWINGS SHALL BE AS FOLLOWS:
 - PILES _____ 60 mm
 - PRECASTED BEAMS _____ 30 mm
 - REMAINING ELEMENTS _____ 40 mm
 6. STEEL USED OF GRADE 400 MPa.

REINFORCEMENT NOTATION :

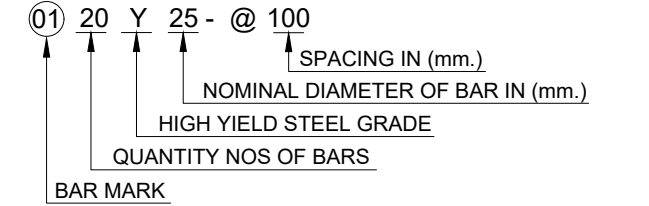

ABBREVIATIONS:

P	PILE	STAGG.	STAGGERED
AX.	AXIS	S.B.	SIDE BAR
N.T.S.	NOT TO SCALE	ST.	STARTER BAR
B	BOTTOM		
	TOP		
ADD.	ADDITIONAL		
O.S.	OUTER STIRRUP		
I.S.	INNER STIRRUP		

DESIGN DRAWINGS REFS :


TTTP-GNR-GH1-WES-EDDW-00005-00008	
TTTP-GNR-GH1-WES-EDDW-00011-00016	
TTTP-GNR-GH1-WES-EDDW-00026	

SPECIFICATIONS REFS :

GEG-ENG-SPC-0000-TRR-005-04	

00	ISSUED FOR INFORMATION	A.A.	20-01-2026
REV.	DESCRIPTION	DRAWN BY	DATE

EL GHYRAN BRIDGE - BRIDGE 01

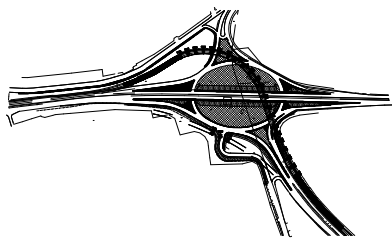

KEY PLAN:

OWNER :




OWNER'S CONSULTANT :



CONTRACTOR:



PROJECT :

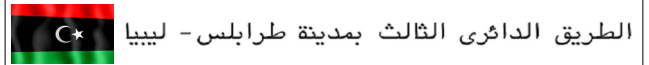

SHOP DRAWING TITLE :

EL GHYRAN // EL GHYRAN BRIDGE 01
TYPICAL PILE REINFORCEMENT DETAILS
FOR AXIS (A"1-2") (1/1)

Dwg.No:	TTRR-GHY-GHY1-OHRNJV-CDF-05-EDWG-00006		
REVISION	00	DRAWN	A.A
SCALE	AS SHOWN	REVIEWED	A.E.
DATE	JAN.-2026	APPROVED	K.N.