



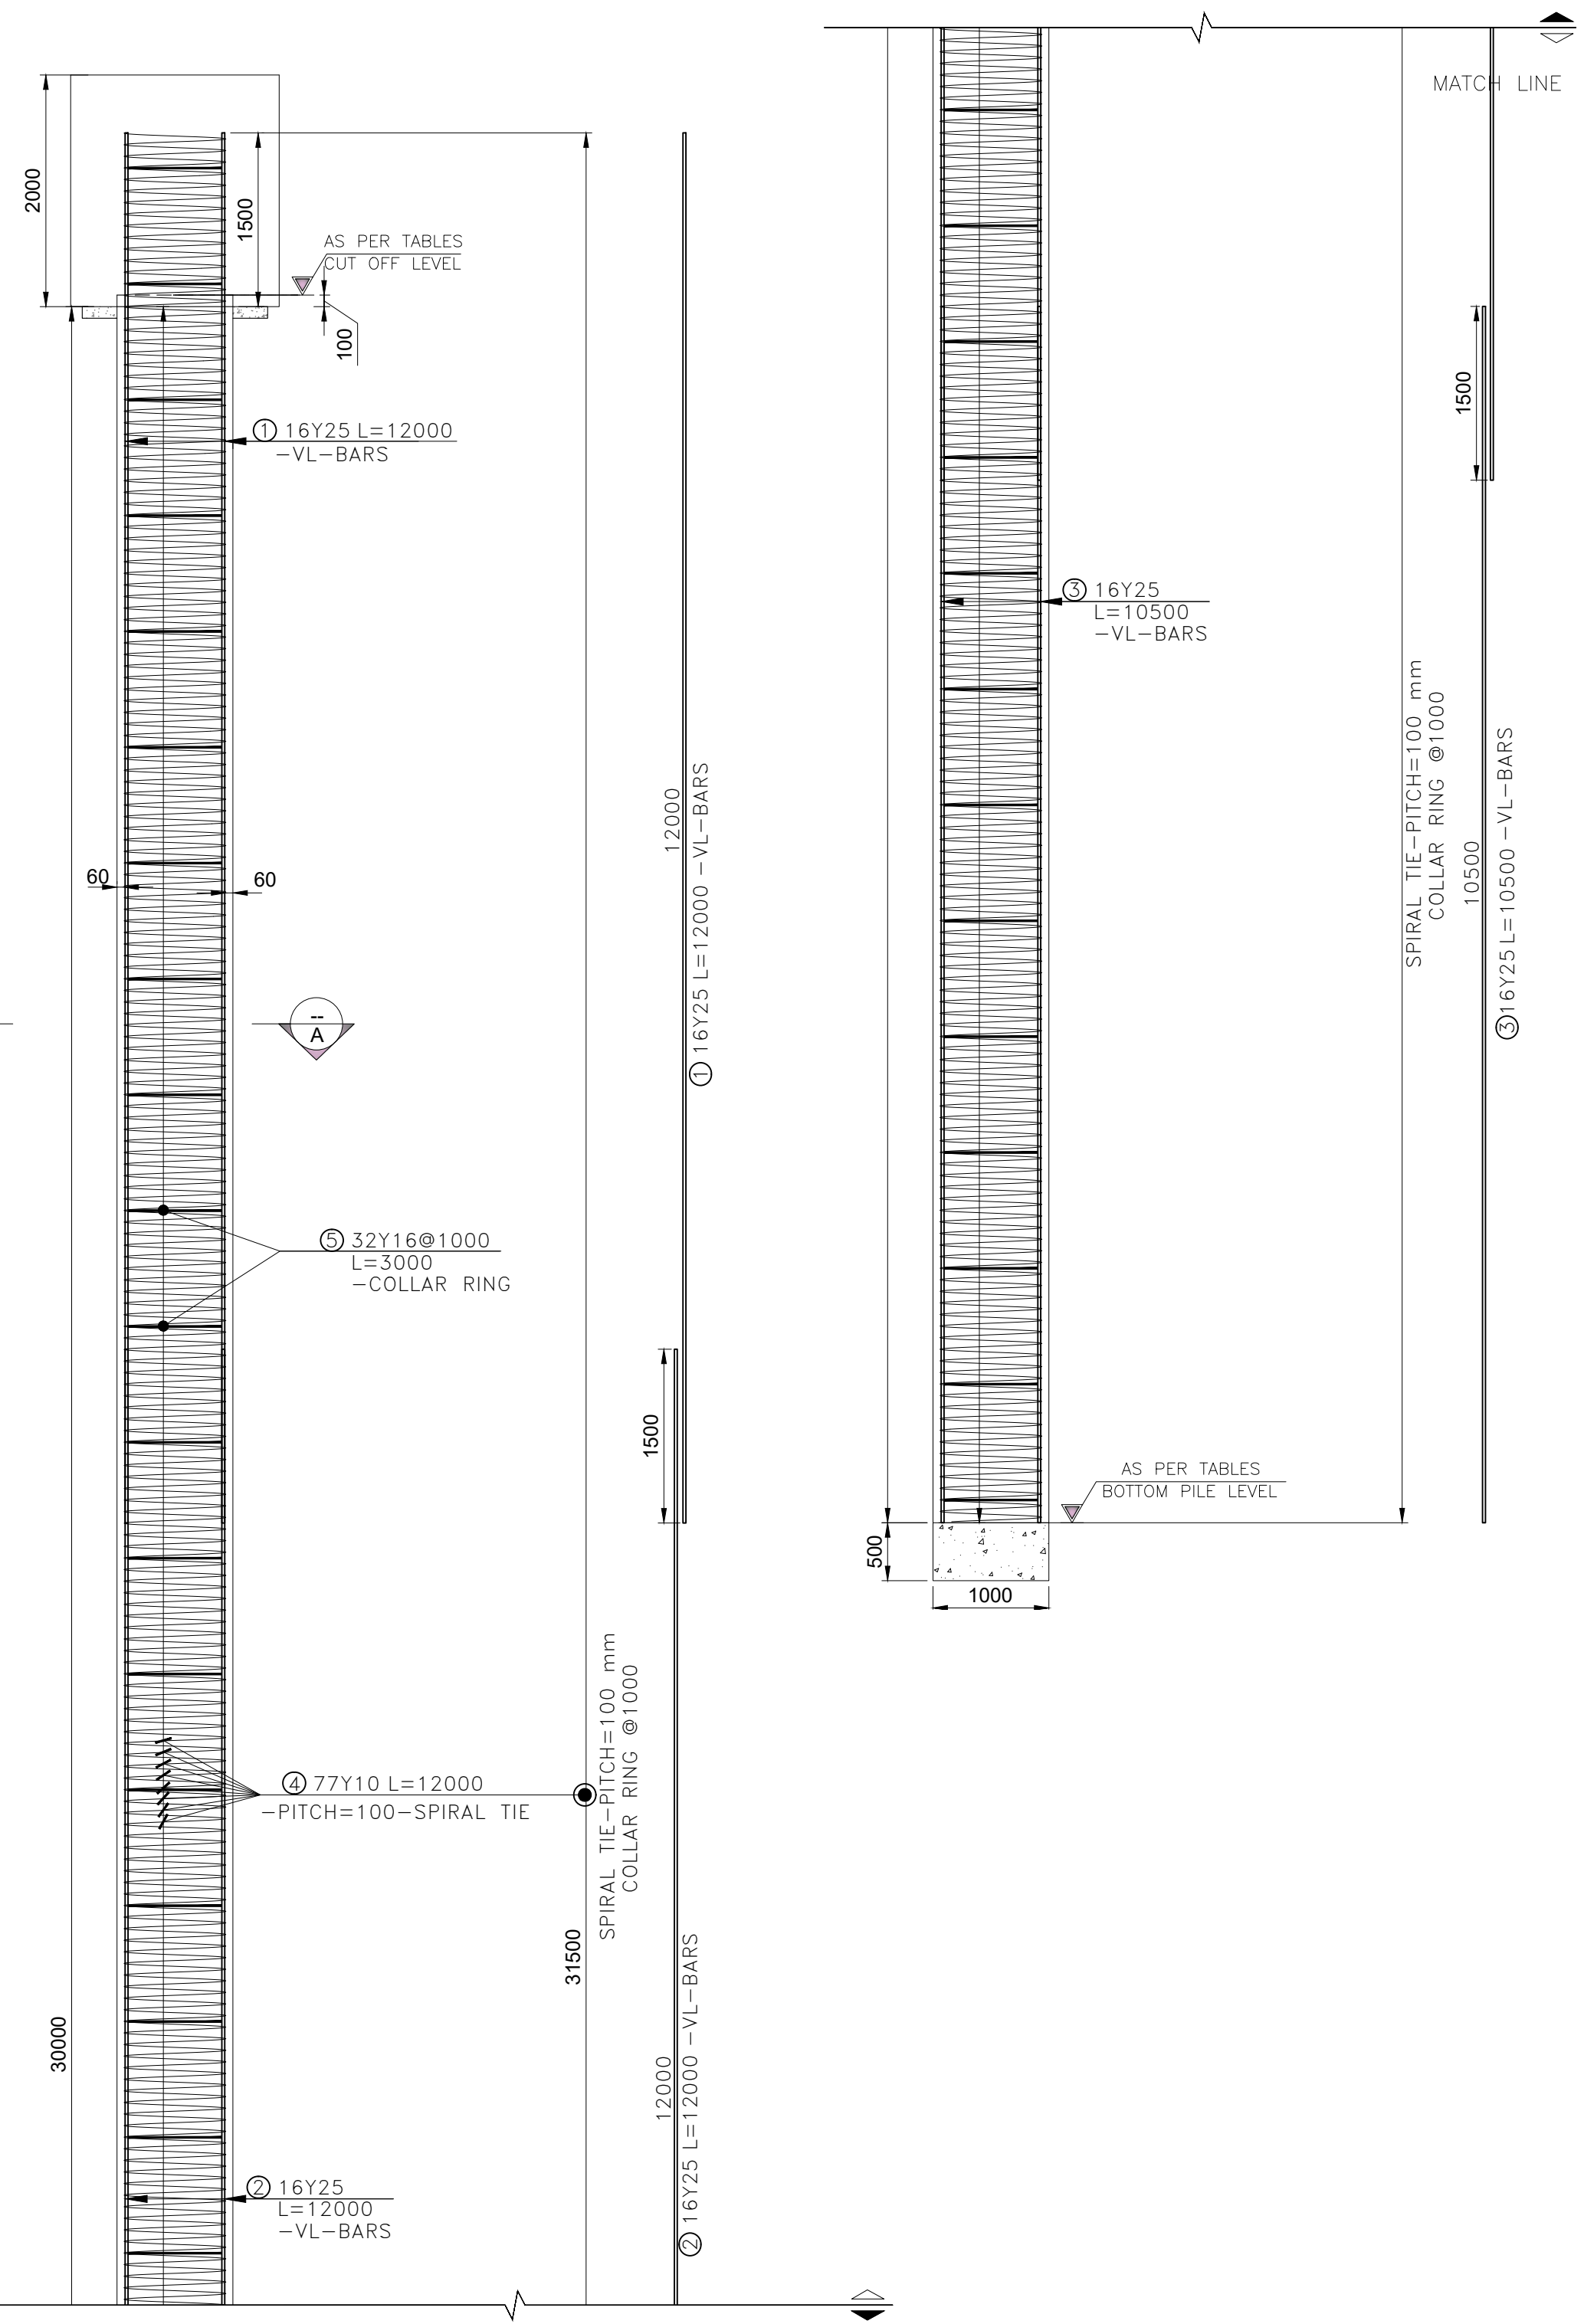

MATERIAL TABLE			
CONCRETE:	EN1992-1-1	EN206-1	MINIMUM COVER
PILES	C25/30	XC2	6cm
PRE CASTED BEAMS:	C35/45	XC4	3cm
REMAINING ELEMENTS	C30/37	XC4	4cm
STEEL:			
REINFORCEMENT STEEL	EN10080-S400C (fyk = 400 MPa - EN 1992-1-1)		
PRESTRESS STEEL	EN10138-3-Y-1860S7-15,7 (S=1,50 cm² - fyd = 1426 MPa)		

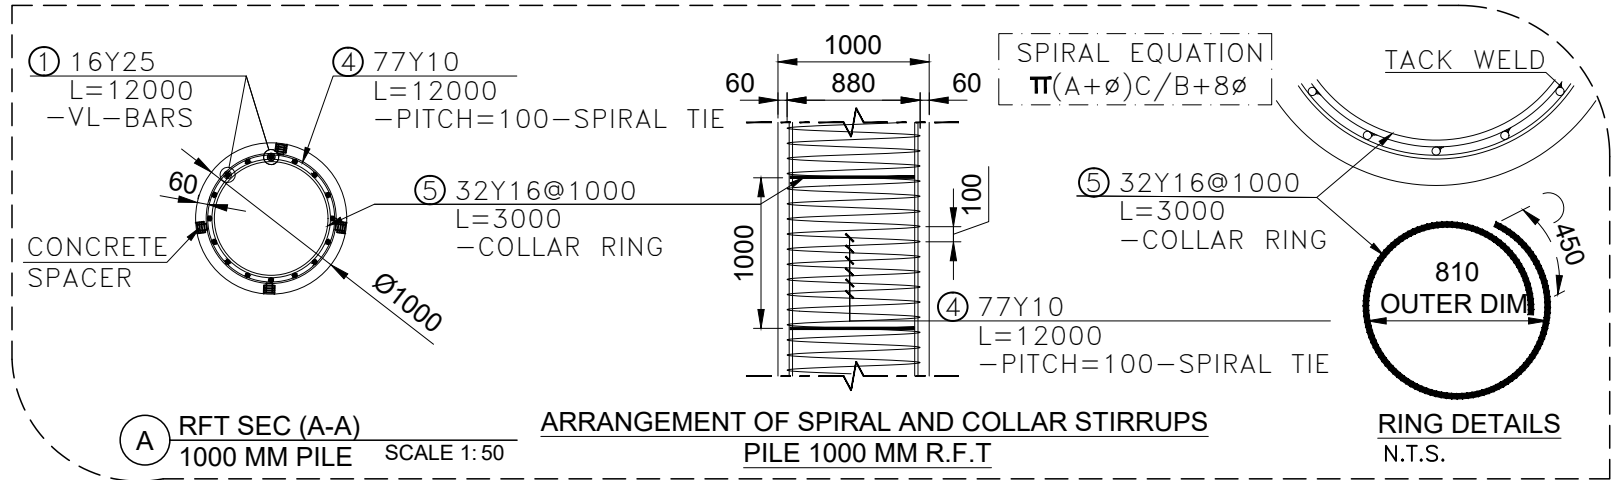

- NOTES:-**
1. ALL DIMENSIONS ARE IN MILLIMETERS UNLESS OTHERWISE SPECIFIED.
 2. ALL DIMENSIONS AND LEVELS MUST BE CHECKED WITH THE PLANNING DRAWINGS.
 3. DO NOT MEASURE FROM DRAWINGS. ALL DIMENSION SHOULD BE READ OR COMPUTED.
 4. COMPRESSIVE STRENGTH OF REINFORCED CONCRETE SHALL BE NOT LESS THAN THESE VALUES :
 - PILES C25/30
 - PRECASTED BEAMS C35/45
 - REMAINING ELEMENTS C30/37
 5. MINIMUM CONCRETE COVER FOR REINFORCEMENT UNLESS OTHERWISE INDICATED ON DRAWINGS SHALL BE AS FOLLOWS:
 - PILES 60 mm
 - PRECASTED BEAMS 30 mm
 - REMAINING ELEMENTS 40 mm
 6. STEEL USED OF GRADE 400 MPA.

REINFORCEMENT NOTATION :

01 20 Y 25 - @ 100

SPACING IN (mm.)

NOMINAL DIAMETER OF BAR IN (mm.)

HIGH YIELD STEEL GRADE

QUANTITY NOS OF BARS



BAR MARK

ABBREVIATIONS:			
P	PILE	STAGG.	STAGGERED
AX.	AXIS	S.B.	SIDE BAR
N.T.S.	NOT TO SCALE	ST.	STARTER BAR
B	BOTTOM		
T	TOP		
ADD.	ADDITIONAL		
O.S.	OUTER STIRRUP		
I.S.	INNER STIRRUP		

DESIGN DRAWINGS REFS :	
TTPP-GNR-GH1-WES-EDDW-00005-00008	3 - 4 - 1769
TTPP-GNR-GH1-WES-EDDW-00011-00016	
TTPP-GNR-GH1-WES-EDDW-00029-C	
TTRR-GE-CHIB2-EPC1-OHRNJY-HI-TRN-3185-01	

SPECIFICATIONS REFS :	
GEG-ENG-SPC-0000-TRR-005-04	

00	ISSUED FOR INFORMATION	A.A.	09-02-2026
REV.	DESCRIPTION	DRAWN BY	DATE

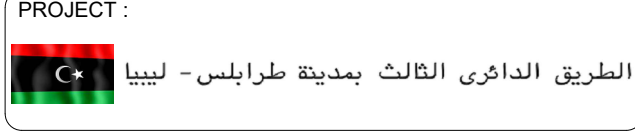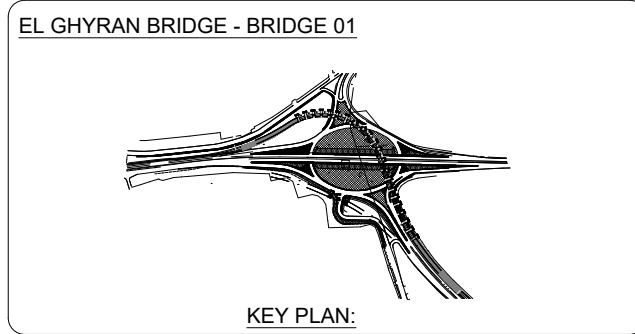

SHOP DRAWING TITLE :

EL GHYRAN // EL GHYRAN BRIDGE 01

TYPICAL PILE REINFORCEMENT DETAILS

FOR AXIS ((P"1-6"-P"1-8")) (1/2)

Dwg.No:	TTRR-GHY-GHY1-OHRNJY-CDF-05-EDWG-00007		
REVISION	01	DRAWN	O.G
SCALE	AS SHOWN	REVIEWED	K.N
DATE	FEB.-2026	APPROVED	K.N.