


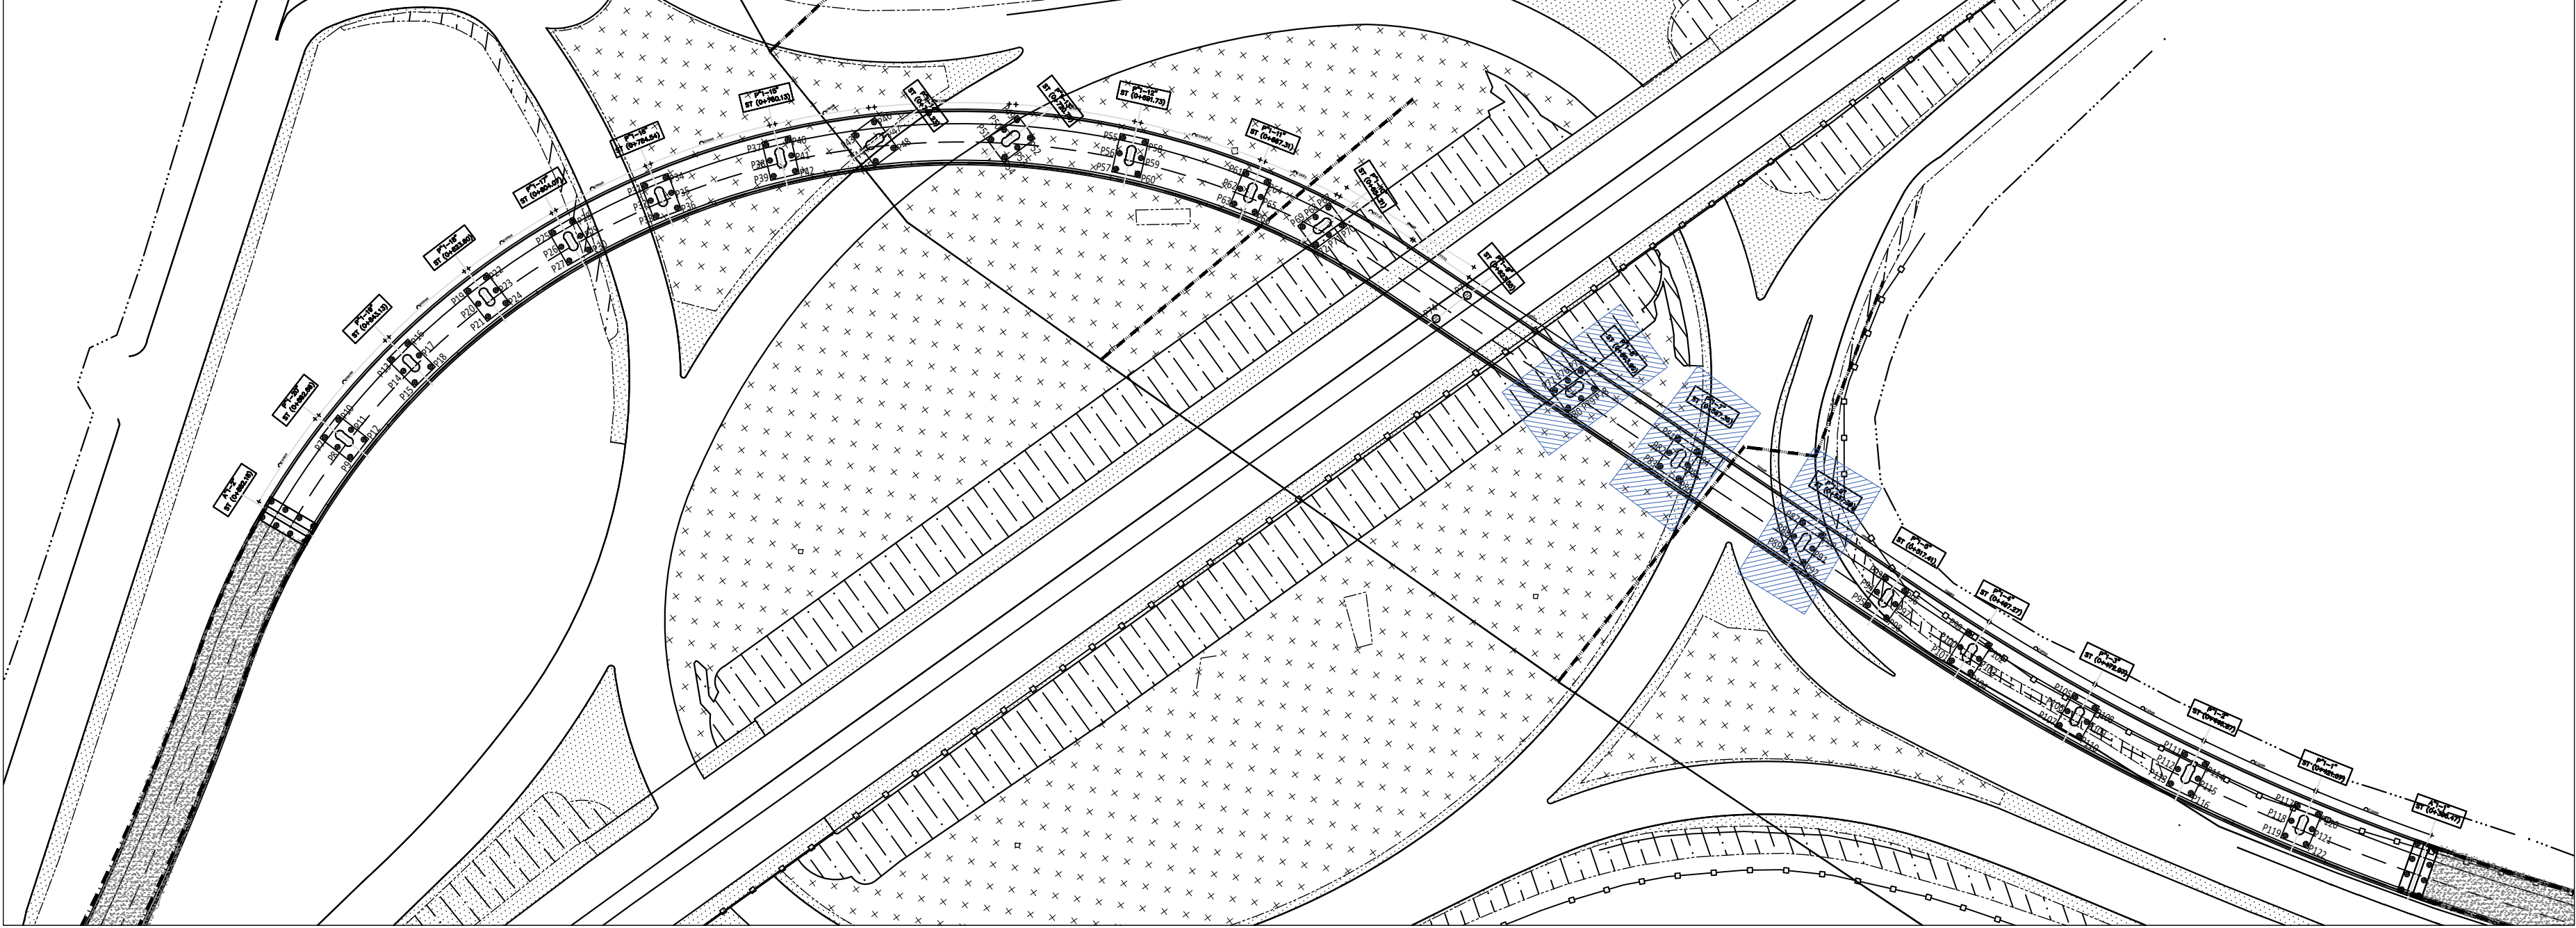

GENERAL PLAN SHOWING ARRANGEMENT OF PILES
FOR EL GHYRAN BRIDGE 01
SCALE 1: 50

PILECAPNAME	PILE NAME	PILEDIAMETER	PILELENGTH	PILEEASTING	PILENORTHING	PILEBOTTOMLEVEL	FOUNDATION BOTTOM LEVEL	CUT-OFF LEVEL
P"1-8"	75	1000 mm	30000 mm	206016.9700	3635198.9593	(-15.088)	(+14.912)	(+15.012)
	76	1000 mm	30000 mm	206013.7700	3635198.9593			
	77	1000 mm	30000 mm	206010.5700	3635198.9593			
	78	1000 mm	30000 mm	206016.9700	3635194.5593			
	79	1000 mm	30000 mm	206013.7700	3635194.5593			
	80	1000 mm	30000 mm	206010.5700	3635194.5593			
P"1-7"	81	1000 mm	30000 mm	206023.9111	3635176.1558	(-16.285)	(+13.715)	(+13.815)
	82	1000 mm	30000 mm	206020.8929	3635175.0927			
	83	1000 mm	30000 mm	206017.8746	3635174.0295			
	84	1000 mm	30000 mm	206025.3729	3635172.0058			
	85	1000 mm	30000 mm	206022.3547	3635170.9426			
	86	1000 mm	30000 mm	206019.3365	3635169.8794			
P"1-6"	87	1000 mm	30000 mm	206034.6798	3635148.1427	(-16.465)	(+13.535)	(+13.635)
	88	1000 mm	30000 mm	206031.6616	3635147.0796			
	89	1000 mm	30000 mm	206028.6434	3635146.0164			
	90	1000 mm	30000 mm	206036.1417	3635143.9927			
	91	1000 mm	30000 mm	206033.1235	3635142.9295			
	92	1000 mm	30000 mm	206030.1052	3635141.8664			

ط 3 - 4 - 1769
TTRR-GE-CHIB2-EPC1-OHRNJV-HI-TRN-3185-01

- NOTES:-
1. ALL DIMENSIONS ARE IN MILLIMETERS UNLESS OTHERWISE SPECIFIED.
 2. ALL DIMENSIONS AND LEVELS MUST BE CHECKED WITH THE PLANNING DRAWINGS.
 3. DO NOT MEASURE FROM DRAWINGS. ALL DIMENSION SHOULD BE READ OR COMPUTED.
 4. COMPRESSIVE STRENGTH OF REINFORCED CONCRETE SHALL BE NOT LESS THAN THESE VALUES :
 - PILES _____ C25/30
 - PRECASTED BEAMS _____ C35/45
 - REMAINING ELEMENTS _____ C30/37
 5. MINIMUM CONCRETE COVER FOR REINFORCEMENT UNLESS OTHERWISE INDICATED ON DRAWINGS SHALL BE AS FOLLOWS:
 - PILES _____ 60 mm
 - PRECASTED BEAMS _____ 30 mm
 - REMAINING ELEMENTS _____ 40 mm
 6. STEEL USED OF GRADE 400 MPA.

REINFORCEMENT NOTATION :
01 20 Y 25 - @ 100
↑ SPACING IN (mm.)
↑ NOMINAL DIAMETER OF BAR IN (mm.)
↑ HIGH YIELD STEEL GRADE
↑ QUANTITY NOS OF BARS
↑ BAR MARK

ABBREVIATIONS:

P	PILE	STAGG.	STAGGERED
AX.	AXIS	S.B.	SIDE BAR
N.T.S.	NOT TO SCALE	ST.	STARTER BAR
B	BOTTOM		
T	TOP		
ADD.	ADDITIONAL		
O.S.	OUTER STIRRUP		
I.S.	INNER STIRRUP		



DESIGN DRAWINGS REFS :

TTPP-GNR-GH1-WES-EDDW-00005-00008	د 3 - 4 - 1769
TTPP-GNR-GH1-WES-EDDW-00011-00016	
TTPP-GNR-GH1-WES-EDDW-00029-C	
TTRR-GE-CHIB2-EPC1-OHRNJV-HI-TRN-3185-01	

SPECIFICATIONS REFS :

GEG-ENG-SPC-0000-TRR-005-04	

00	ISSUED FOR INFORMATION	A.A.	09-02-2026
REV.	DESCRIPTION	DRAWN BY	DATE

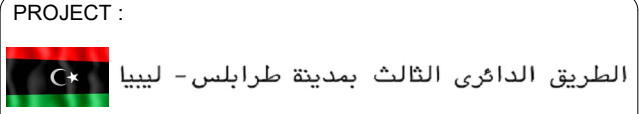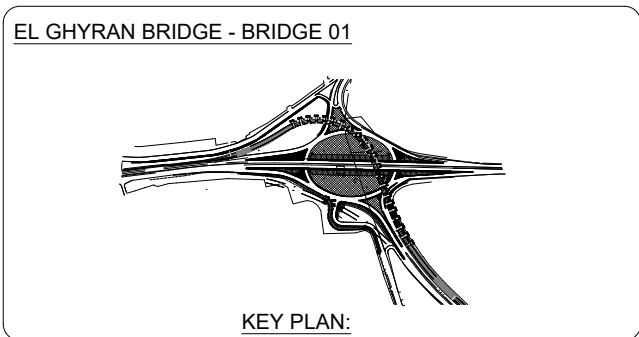

SHOP DRAWING TITLE :

EL GHYRAN // EL GHYRAN BRIDGE 01

TYPICAL PILE REINFORCEMENT DETAILS

FOR AXIS ((P"1-6"-P"1-8"))

(2/2)

Dwg.No:	TTRR-GHY-GHY1-OHRNJV-CDF-05-EDWG-00008		
REVISION	01	DRAWN	O.G
SCALE	AS SHOWN	REVIEWED	K.N
DATE	FEB.-2026	APPROVED	K.N.