


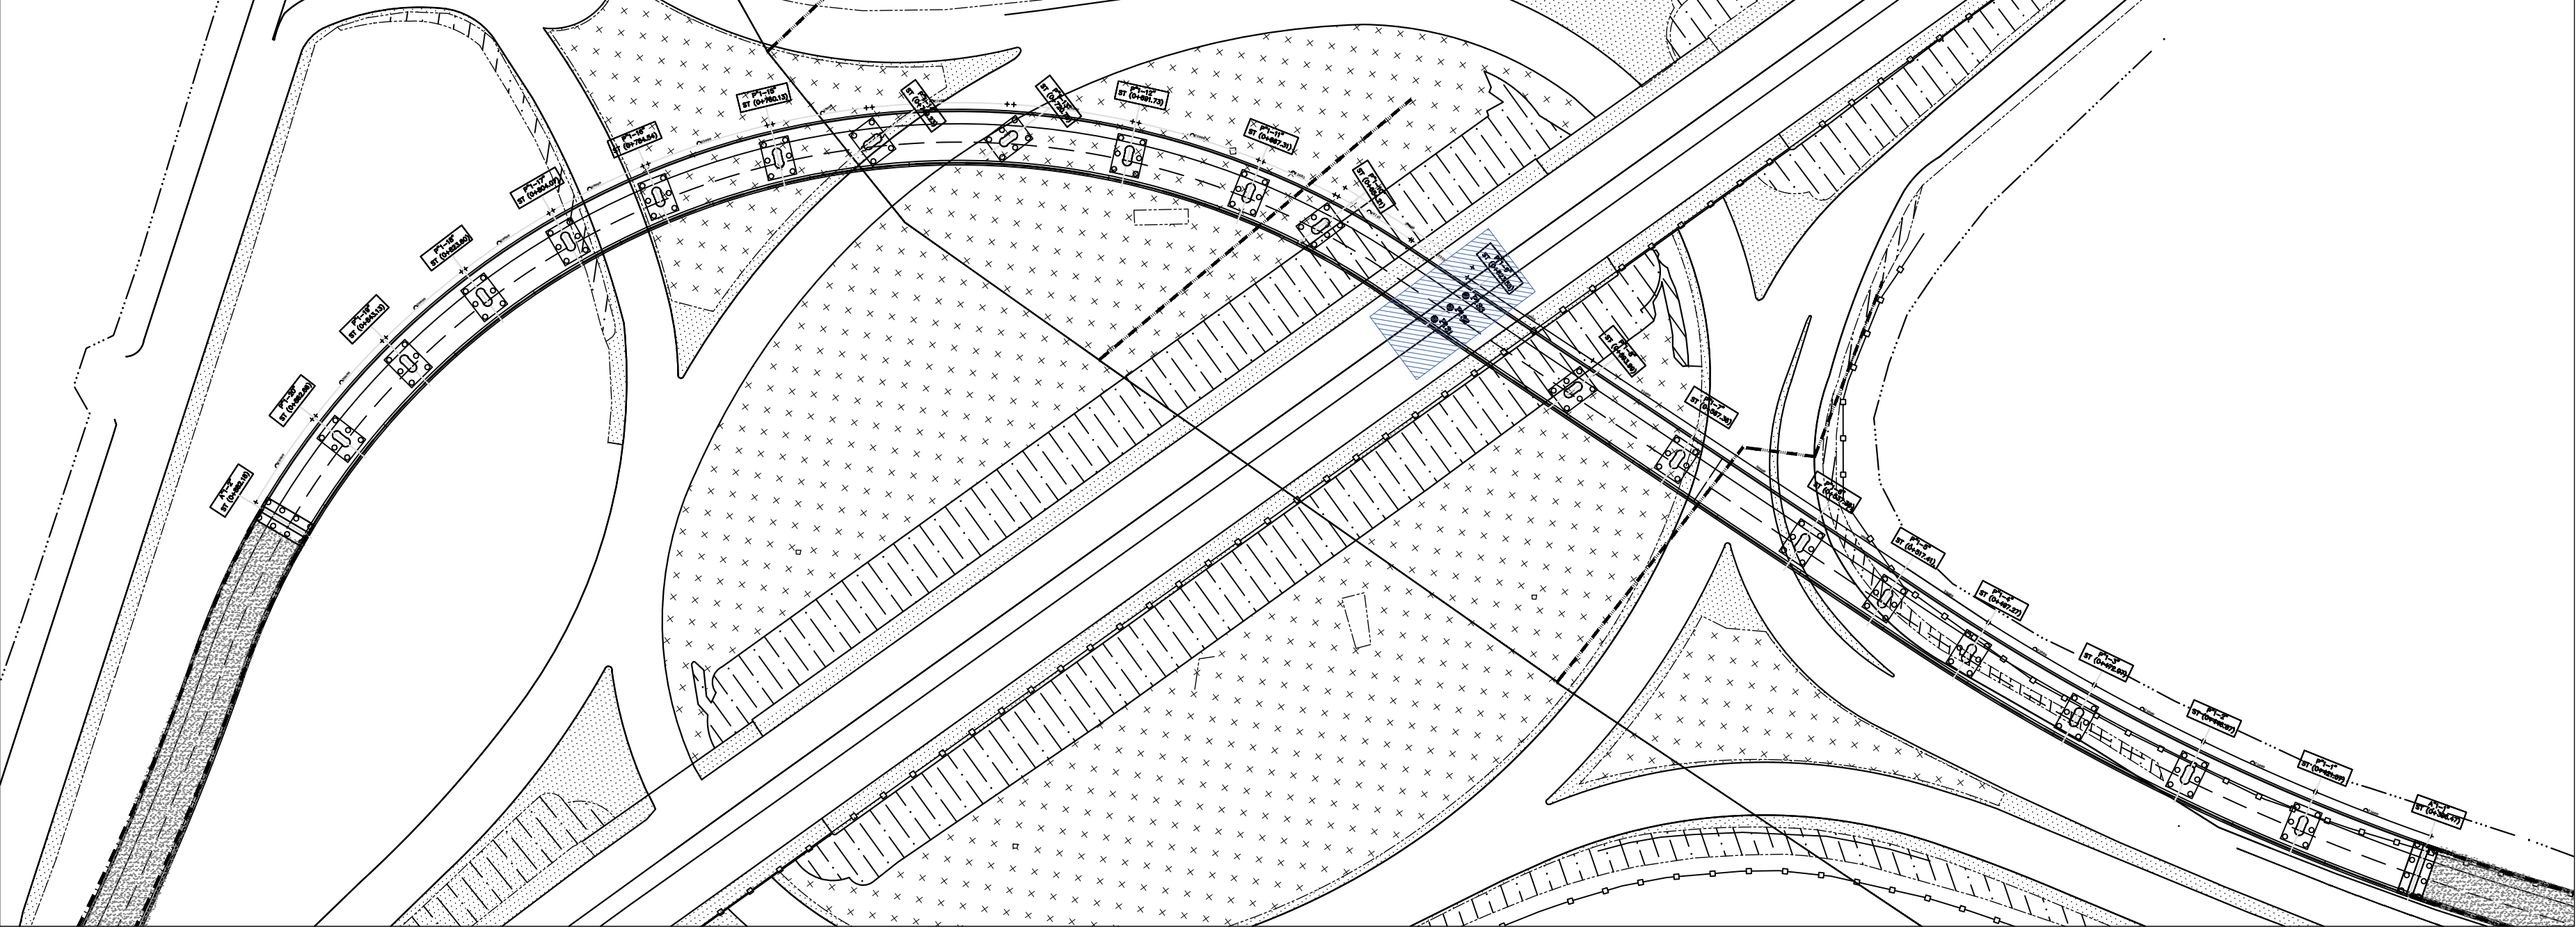

GENERAL PLAN SHOWING ARRANGEMENT OF PILES
FOR EL GHYRAN BRIDGE 01
SCALE 1: 50

PILECAP NAME	PILE NAME	PILE DIAMETER	PILE LENGTH	PILE EASTING	PILE NORTHING	PILE BOTTOM LEVEL	GROUND LEVEL	CUT-OFF LEVEL
P"1-9"	131	1200 mm	29000 mm	206000.0650	3635224.6390	(-5.014)	(+23.986)	(+23.986)
	132	1200 mm	29000 mm	206003.9700	3635224.6390			
	133	1200 mm	29000 mm	206007.8760	3635224.6390			

- NOTES:-
1. ALL DIMENSIONS ARE IN MILLIMETERS UNLESS OTHERWISE SPECIFIED.
 2. ALL DIMENSIONS AND LEVELS MUST BE CHECKED WITH THE PLANNING DRAWINGS.
 3. DO NOT MEASURE FROM DRAWINGS. ALL DIMENSION SHOULD BE READ OR COMPUTED.
 4. COMPRESSIVE STRENGTH OF REINFORCED CONCRETE SHALL BE NOT LESS THAN THESE VALUES :
 - PILES C25/30
 - MONO PILES C30/37
 - PRECASTED BEAMS C35/45
 - REMAINING ELEMENTS C30/37
 5. MINIMUM CONCRETE COVER FOR REINFORCEMENT UNLESS OTHERWISE INDICATED ON DRAWINGS SHALL BE AS FOLLOWS:
 - PILES 60 mm
 - PRECASTED BEAMS 30 mm
 - REMAINING ELEMENTS 40 mm
 6. STEEL USED OF GRADE 400 MPA.

REINFORCEMENT NOTATION :

① 20 Y 25 - @ 100

SPACING IN (mm.)

NOMINAL DIAMETER OF BAR IN (mm.)

HIGH YIELD STEEL GRADE

QUANTITY NOS OF BARS

BAR MARK

ABBREVIATIONS:

P	PILE	STAGG.	STAGGERED
AX.	AXIS	S.B.	SIDE BAR
N.T.S.	NOT TO SCALE	ST.	STARTER BAR
B	BOTTOM		
T	TOP		
ADD.	ADDITIONAL		
O.S.	OUTER STIRRUP		
I.S.	INNER STIRRUP		

DESIGN DRAWINGS REFS :


TTPP-GNR-GH1-WES-EDDW-0020-02	
TTPP-GNR-GH1-WES-EDDW-0064-B	
TTRR-GE-CHIB2-EPC1-OHRNJV-HI-TRN-3115-04	

SPECIFICATIONS REFS :

GEG-ENG-SPC-0000-TRR-005-04	

01	ISSUED FOR INFORMATION	O.G	15-04-2026
00	ISSUED FOR INFORMATION	O.G	07-04-2026
REV.	DESCRIPTION	DRAWN BY	DATE

EL GHYRAN BRIDGE - BRIDGE 01

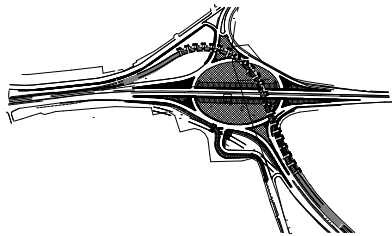

KEY PLAN:

OWNER :




OWNER'S CONSULTANT :



CONTRACTOR:



PROJECT :

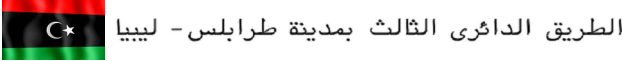

SHOP DRAWING TITLE :

EL GHYRAN // EL GHYRAN BRIDGE 01
TYPICAL PILE REINFORCEMENT DETAILS
FOR AXIS ((P"1-9")
(2/2)

Dwg.No:	TTRR-GHY-GHY1-OHRNJV-CDF-05-EDWG-00014		
REVISION	01	DRAWN	O.G
SCALE	AS SHOWN	REVIEWED	K.N
DATE	APRIL.-2026	APPROVED	K.N.