


NOTES:-

1. ALL DIMENSIONS ARE IN MILLIMETERS UNLESS OTHERWISE SPECIFIED
2. ALL DIMENSIONS AND LEVELS MUST BE CHECKED WITH PLANS.
3. DO NOT MEASURE FROM DRAWINGS. ALL DIMENSION SHOULD BE READ OR COMPUTED.
4. COMPRESSIVE STRENGTH OF REINFORCED CONCRETE SHALL BE NOT LESS THAN THESE VALUES :
  - PILES \_\_\_\_\_ C25/30
  - PRECASTED BEAMS \_\_\_\_\_ C35/45
  - REMAINING ELEMENTS \_\_\_\_\_ C30/37
5. MINIMUM CONCRETE COVER FOR REINFORCEMENT UNLESS OTHERWISE INDICATED ON DRAWINGS SHALL BE AS FOLLOWS:
  - PILES \_\_\_\_\_ 60 mm
  - PRECASTED BEAMS \_\_\_\_\_ 30 mm
  - REMAINING ELEMENTS \_\_\_\_\_ 40 mm
6. STEEL USED OF GRADE 400 MPa.

REINFORCEMENT NOTATION :

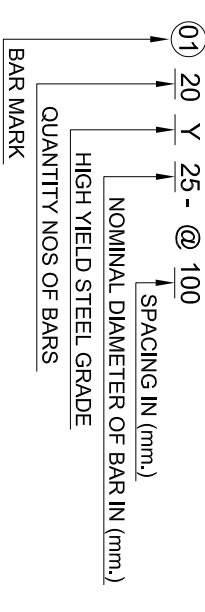

ABBREVIATIONS:

| P        | PILE            | B.O.X. | BOTTOM OF CROSS |
|----------|-----------------|--------|-----------------|
| A.X.     | AXIS            | CONC.  | CONCRETE        |
| N.T.S.   | NOT TO SCALE    | DIM.   | DIMENSION       |
| F.       | FOOTING CORNER  |        |                 |
| C.       | COLUMN          |        |                 |
| B.O.     | BOTTOM OF       |        |                 |
| MID.O.X. | MIDDLE OF CROSS |        |                 |
| T.O.X.   | TOP OF CROSS    |        |                 |

DESIGN DRAWINGS REFS. :


TTRR-PH4-IC20-OHRNUV-CDS-29-ED0G-000001  
TTRR-PH4-IC20-OHRNUV-CDS-29-ED0G-000002

SPECIFICATIONS REFS. :

GEG-ENG-SFC-0000-TRR-004-03  
GEG-ENG-SFC-0000-GEN-001

| REV. | DESCRIPTION            | DATE            |
|------|------------------------|-----------------|
| 00   | ISSUED FOR INFORMATION | M.H. 15-06-2025 |

IC20 - PHASE (4)

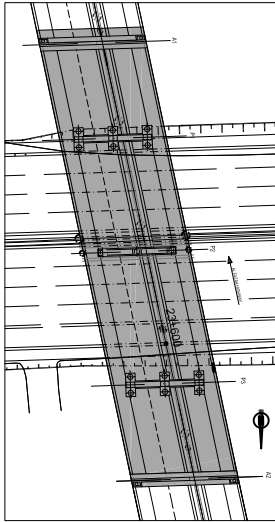

KEY PLAN

OWNER :



OWNER'S CONSULTANT :




Hill International

CONTRACTOR:



PROJECT :

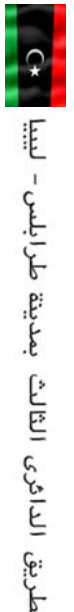

المشروع: الطريق الدائري الثالث بمدينة طرابلس - ليبيا



SHOP DRAWING TITLE :

PHASE 4 // IC20  
BEARINGS LAYOUT PLAN FOR  
BRIDGE (IC20 )

(1/1)

Dwg.No: TTRR-PH4-IC20-OHRNUV-CCR-02-EDWG-00001

| REVISION | 00         | DRAWN    | M.H.  |
|----------|------------|----------|-------|
| SCALE    | AS SHOWN   | REVIEWED | M.AY. |
| DATE     | JUNE.-2025 | APPROVED | S.R.  |

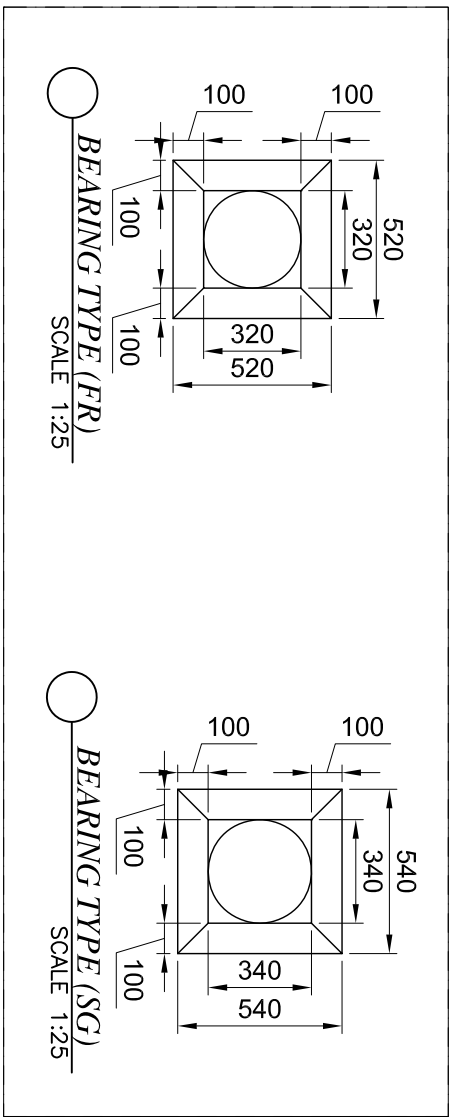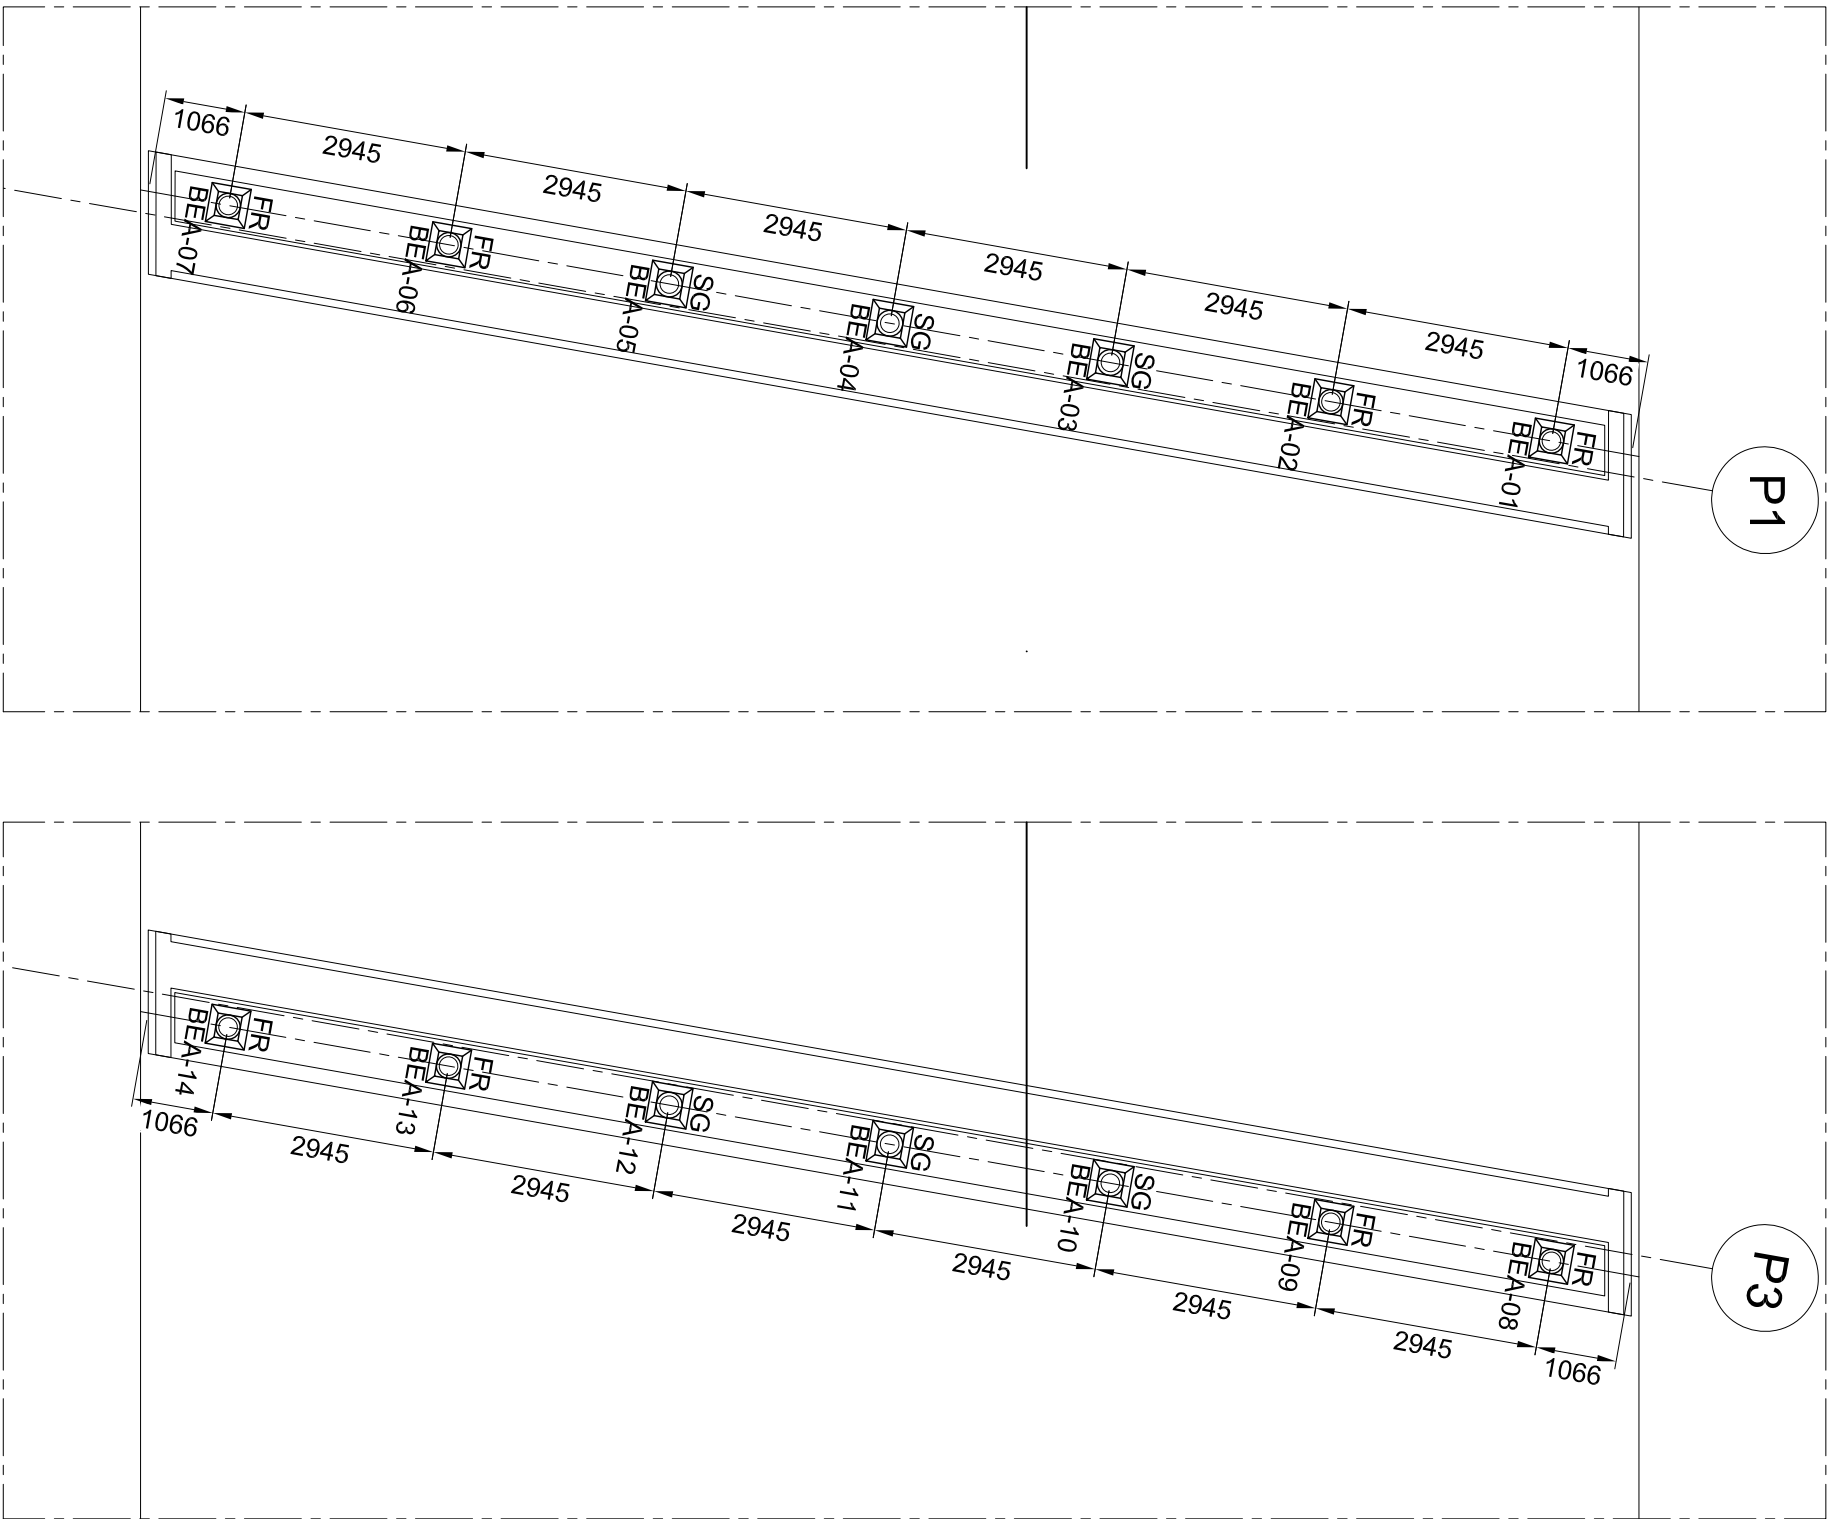

| COORDINATES |            |             |
|-------------|------------|-------------|
| POINTS      | EASTING    | NORTHING    |
| BEA-01      | 224479.044 | 3642239.036 |
| BEA-02      | 224481.987 | 3642239.130 |
| BEA-03      | 224484.931 | 3642239.223 |
| BEA-04      | 224487.874 | 3642239.317 |
| BEA-05      | 224490.818 | 3642239.411 |
| BEA-06      | 224493.761 | 3642239.504 |
| BEA-07      | 224496.705 | 3642239.598 |
| BEA-08      | 224469.202 | 3642285.691 |
| BEA-09      | 224472.145 | 3642285.787 |
| BEA-10      | 224475.089 | 3642285.883 |
| BEA-11      | 224478.032 | 3642285.979 |
| BEA-12      | 224480.976 | 3642286.076 |
| BEA-13      | 224483.919 | 3642286.172 |
| BEA-14      | 224486.863 | 3642286.268 |